





SIDE ELEVATION

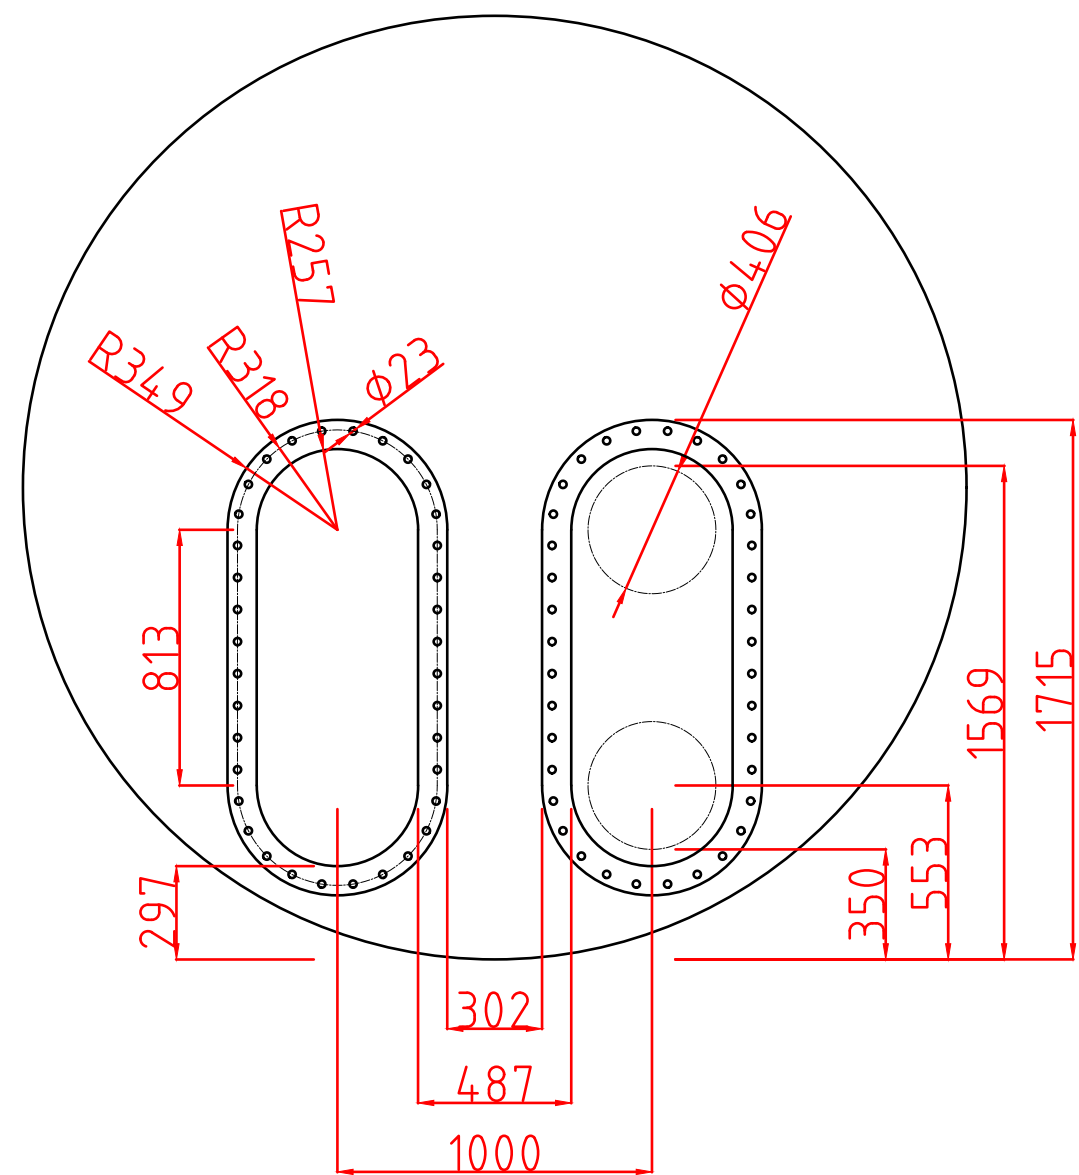

FRONT ELEVATION

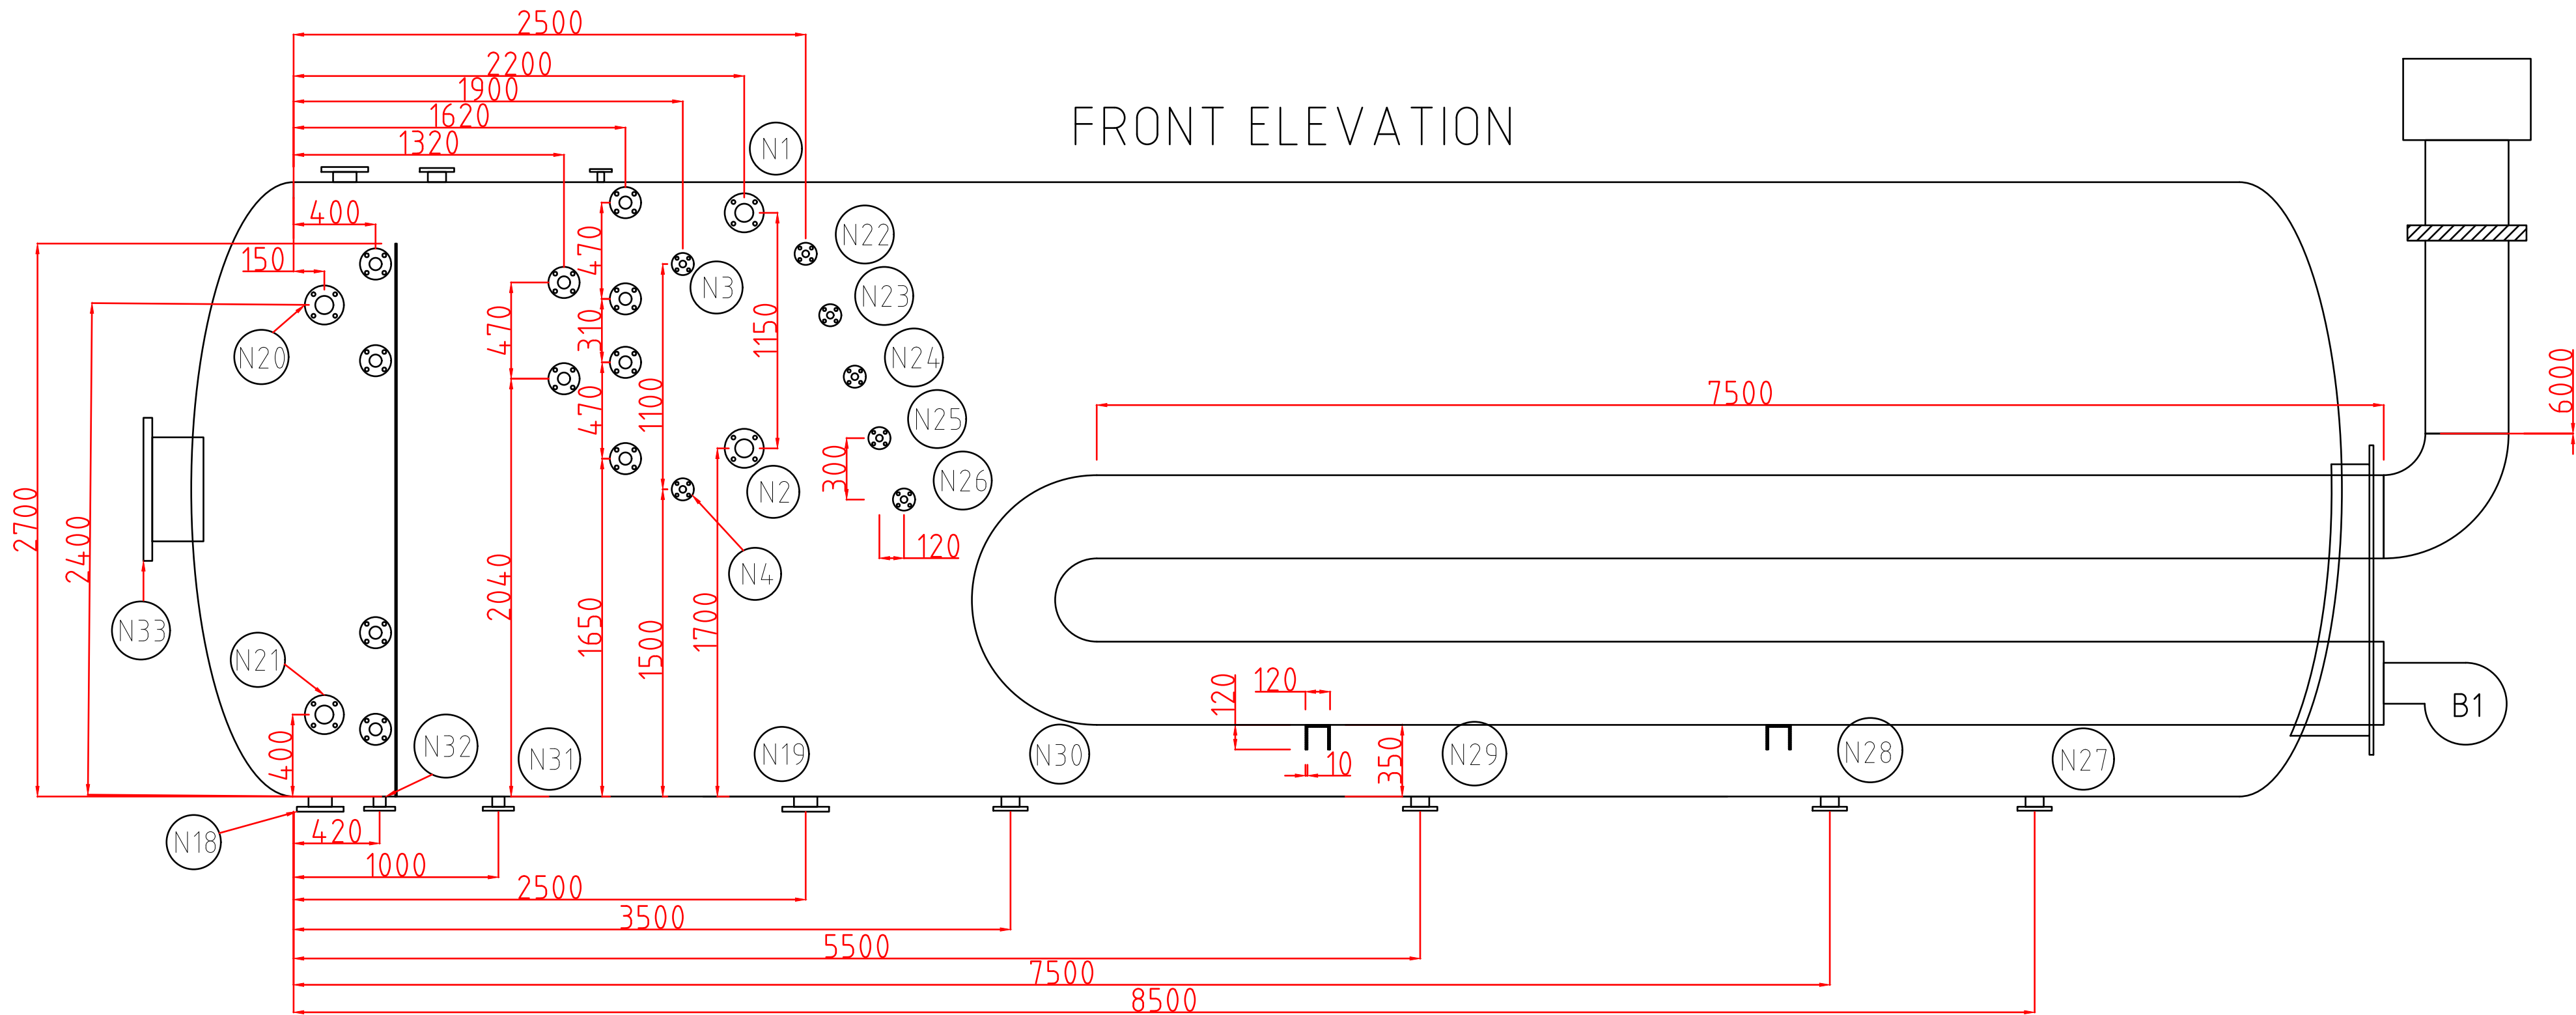

PLAN VIEW

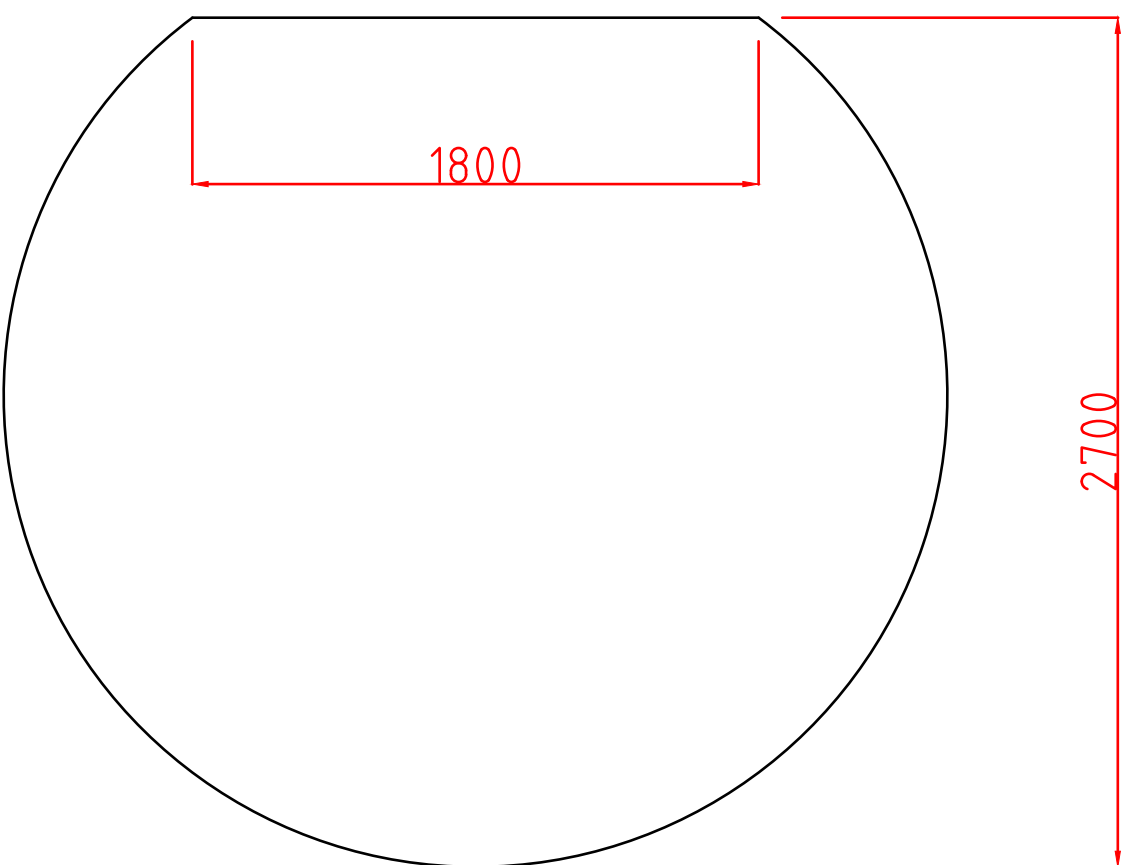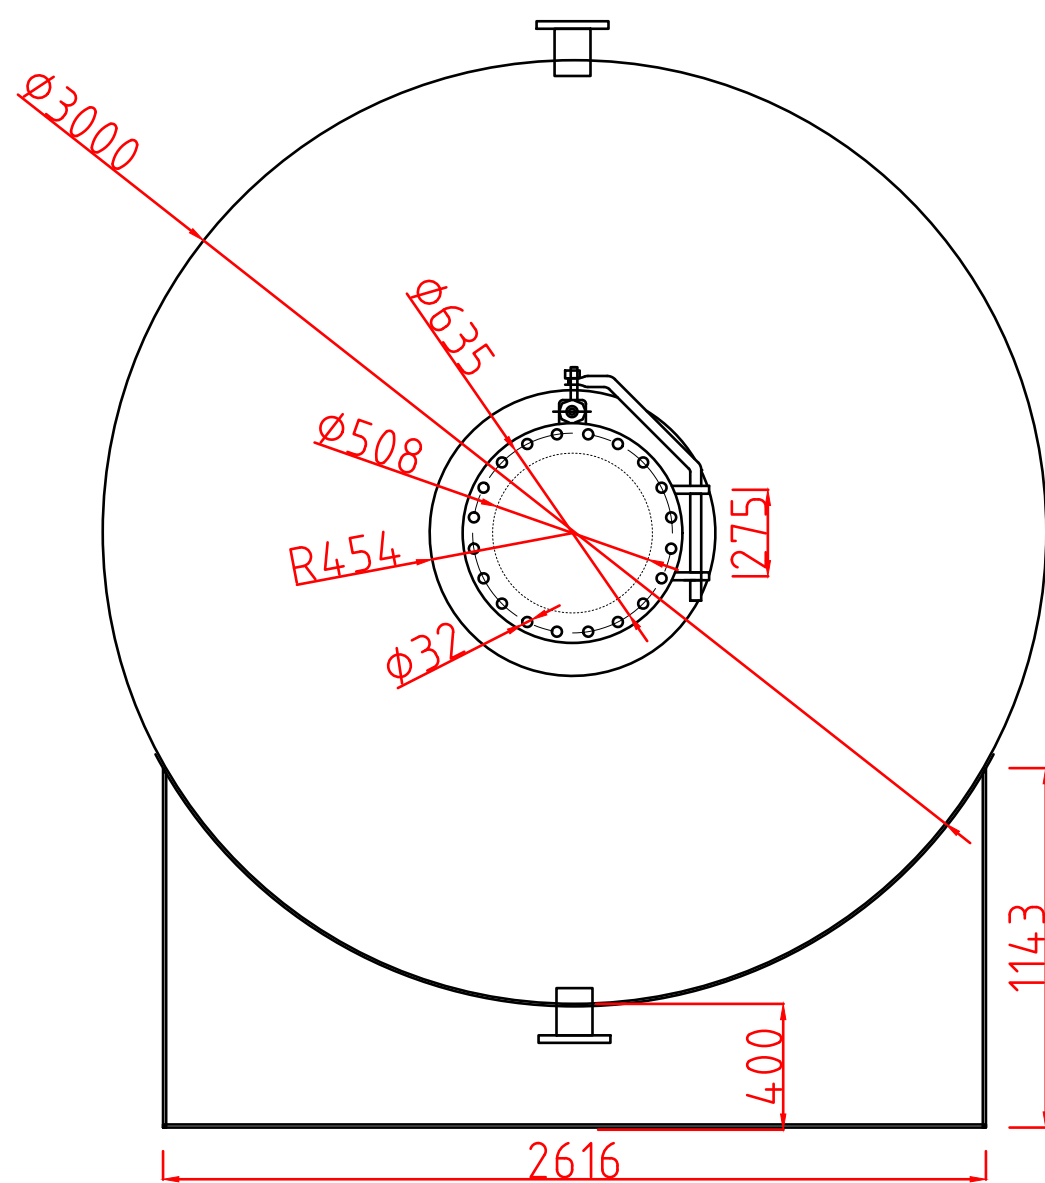

NOZZLE	DIMS	QTY	DESCRIPTION	SPECIFICATION
N1	3"	1	HIGH HIGH LEVEL SWITCH	SA106-GR.B SA105-B16.5
N2	3"	1	LOW LOW LEVEL SWITCH	SA106-GR.B SA105-B16.5
N3 - N4	1"	2	TEMPERATURE TRANSMITTER	SA106-GR.B SA105-B16.5
N5 - N14	2"	10	SIGHT GLASS	SA106-GR.B SA105-B16.5
N15	3"	1	PRESSURE SAFETY VALVE	SA106-GR.B SA105-B16.5
N16	4"	1	GAS OUTLET	SA106-GR.B SA105-B16.5
N17	2"	1	PRESSURE GAUGE	SA106-GR.B SA105-B16.5
N18	4"	1	OIL OUTLET	SA106-GR.B SA105-B16.5
N19	4"	1	CRUDE OIL INPUT	SA106-GR.B SA105-B16.5
N20 - N21	3"	2	OIL LEVEL SWITCHES	SA106-GR.B SA105-B16.5
N22 - N26	1"	5	SAMPLING NOZZLE	SA106-GR.B SA105-B16.5
N27	3"	1	FRESH WATER INLET	SA106-GR.B SA105-B16.5
N28 - N31	3"	4	WATER DRAIN	SA106-GR.B SA105-B16.5
N32	2"	1	WATER DRAIN	SA106-GR.B SA105-B16.5
N33	20"	1	MANHOLE NECK ROLLED PLATE 10MM	SA516-GR.70 SA105-B16.5
N34 - N35	20"	2	FIRETUBE FLANGE OPENING	SA516-GR.70 SA105-B16.5
B1 - B2	-	2	BURNERS	-

APPROVED FOR CONSTRUCTION

DATE: 10-May-26


PETROTEC


INDUSTRIAL ENGINEERING COMPANY

HEATER TREATER

GENERAL ASEMBLY - MECHANICAL DETAILS

VESSEL MATERIAL	VESSEL THICKNESS	LENGTH	DIAMETER	SERIAL NO.
SA-283 Grade C	12 MM	9.5 M	3.04M	PT-009
ENDCAP MATERIAL	ENDCAP THICKNESS	ENDCAP TYPE	TOTAL WEIGHT	
SA-283 Grade C	12 MM	ELLIPTICAL	19 TON	
DWG. NO.	DRAWN BY	DESIGNED BY	REV.	DATE
PT-009-01	ENG. I.H	ENG. TAREK HAMMAD	01	04-May-26

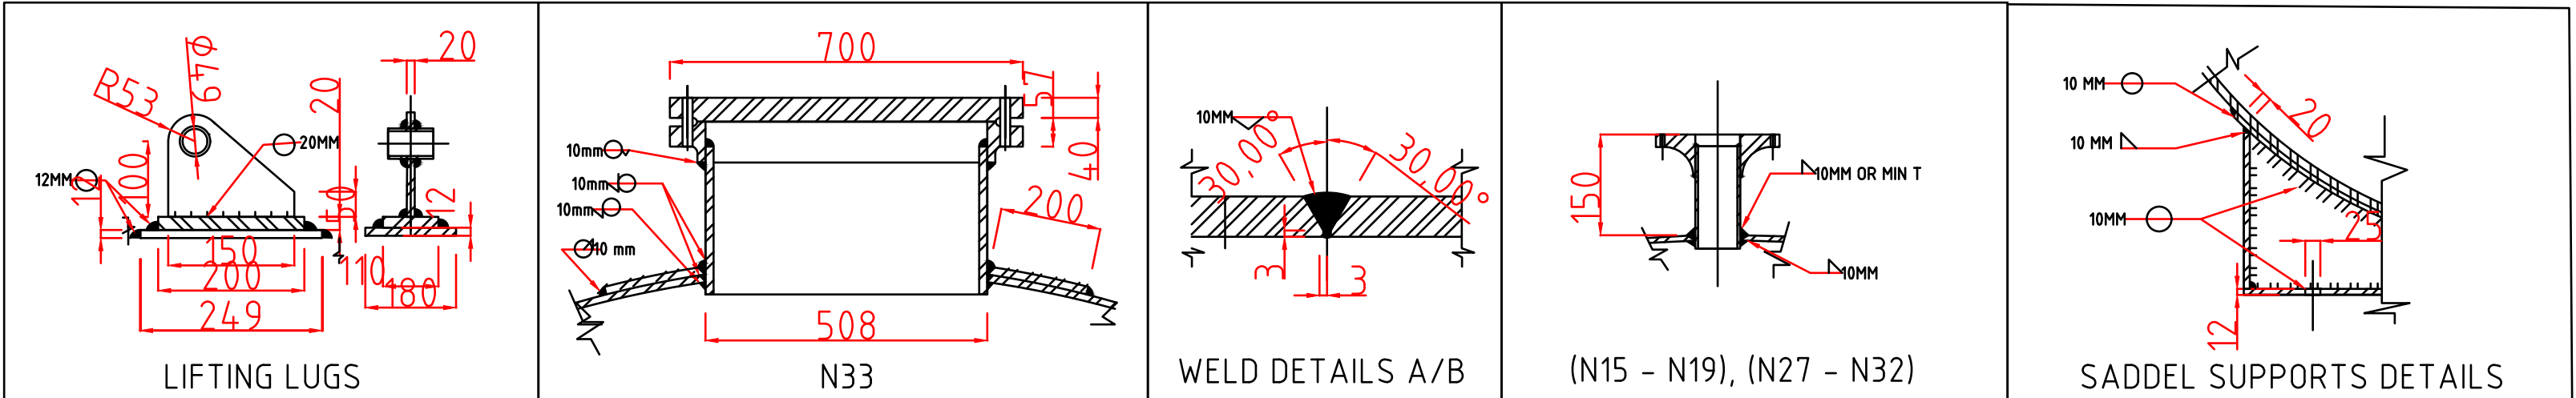

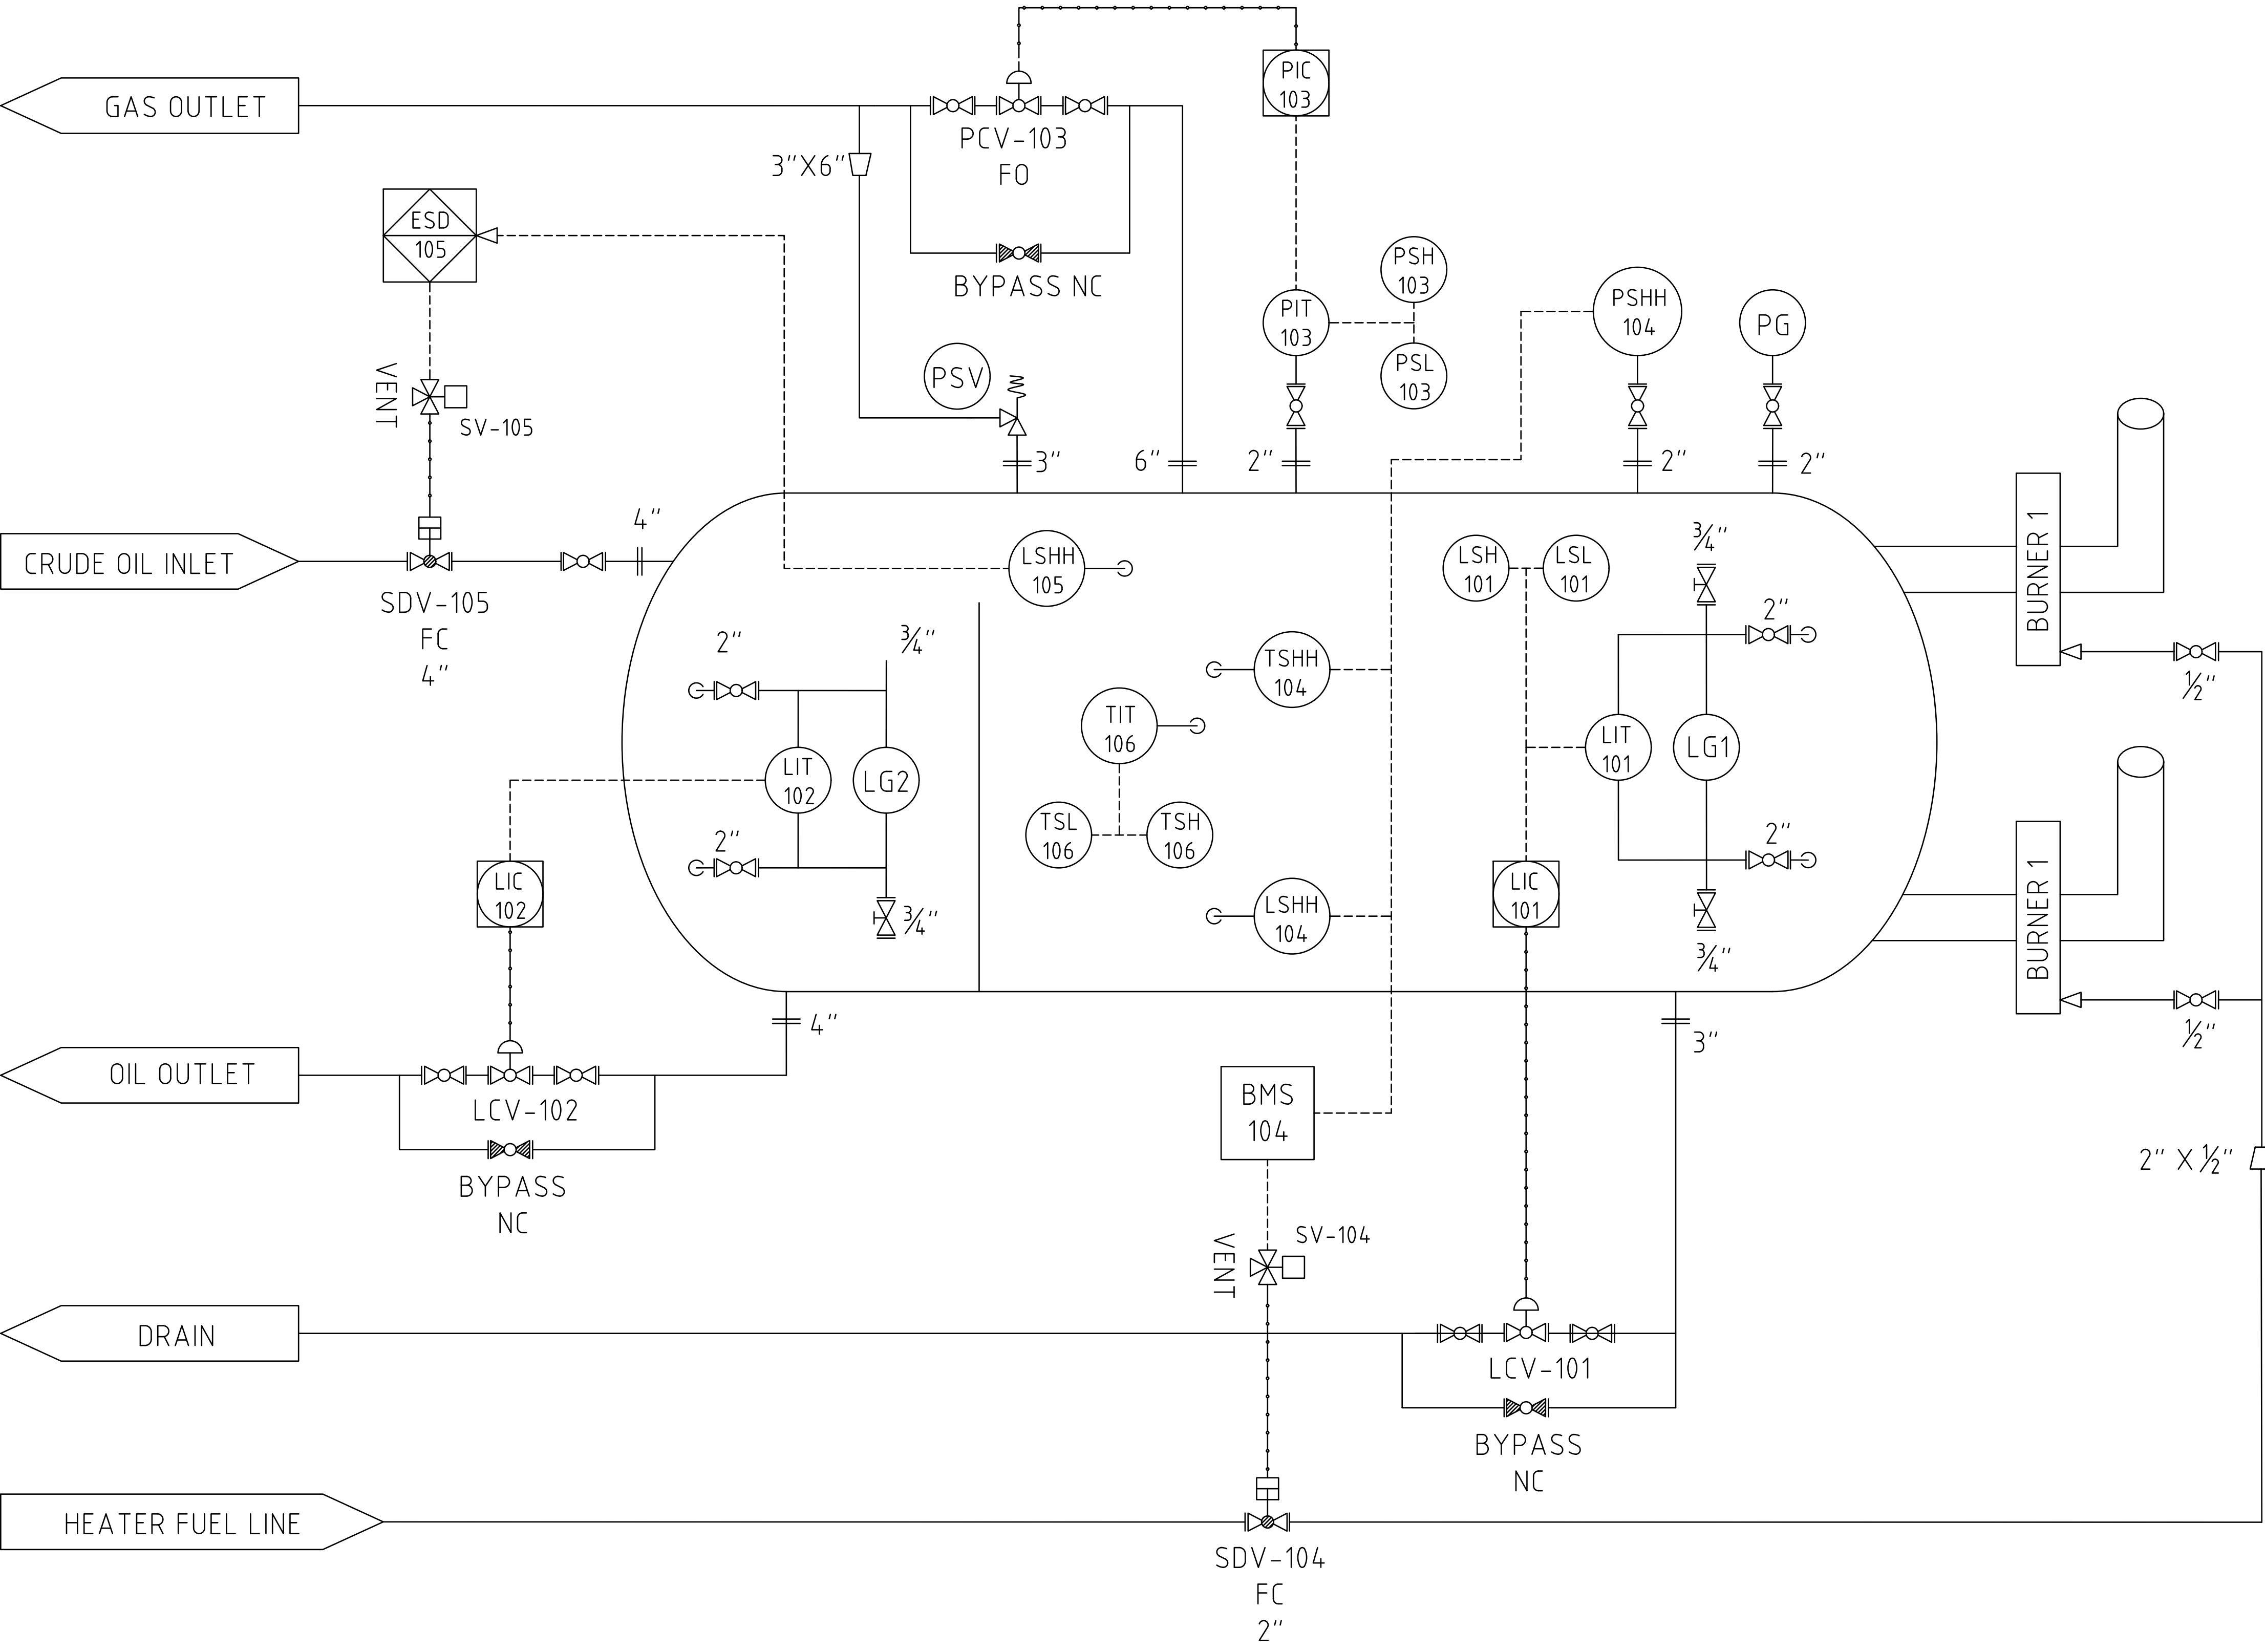

H-101
HT - HEATER TREATER
3.04M OD × 9.5M LENGTH
D/OP DUTY: 4/4 MMBTU/HR
D/OP PRESSURE: 65/ - PSIG
D/OP CAPACITY: 15000/±10000 BPD

SHUTDOWN TRIPS

LSLL-104 — Low-Low Liquid Level
TSHH-104 — High-High Temperature.
PSHH -104 — High-High Pressure.
LSHH - 105 — High-High Liquid Level (INLET)

PROCESS ALARMS

PSH-103 — High pressure alarm.
PSL-103 — Low pressure alarm.
LSH-102 — High liquid level alarm.
LSL-102 — Low liquid level alarm.
TSH-106 — High temperature.
TSL-106 — High temperature.

VALVES		LINE SYMBOLS:	
BALL (SHUTDOWN)		PROCESS LINE	
GLOBE (CONTROL)		SIGNAL LINE	
BALL (PNEUMATIC)		AIR LINE	
SOLENOID VALVE			
GAUGE COCK			

PETROTEC
INDUSTRIAL ENGINEERING COMPANY

DRAWING TITLE
PIPING AND INSTRUMENTATION DIAGRAM
P&ID FOR HEATER TREATER H-101

DWG. NO.	DRAWN BY	DESIGNED BY	DATE
PT-009-03	ENG. I.H	ENG. TAREK HAMMAD	30-May-26

PROPERTY OF PETROTEC. REPRODUCTION OR UNAUTHORIZED USE WITHOUT
PRIOR WRITTEN APPROVAL IS PROHIBITED AND SUBJECT TO LEGAL ACTION.