


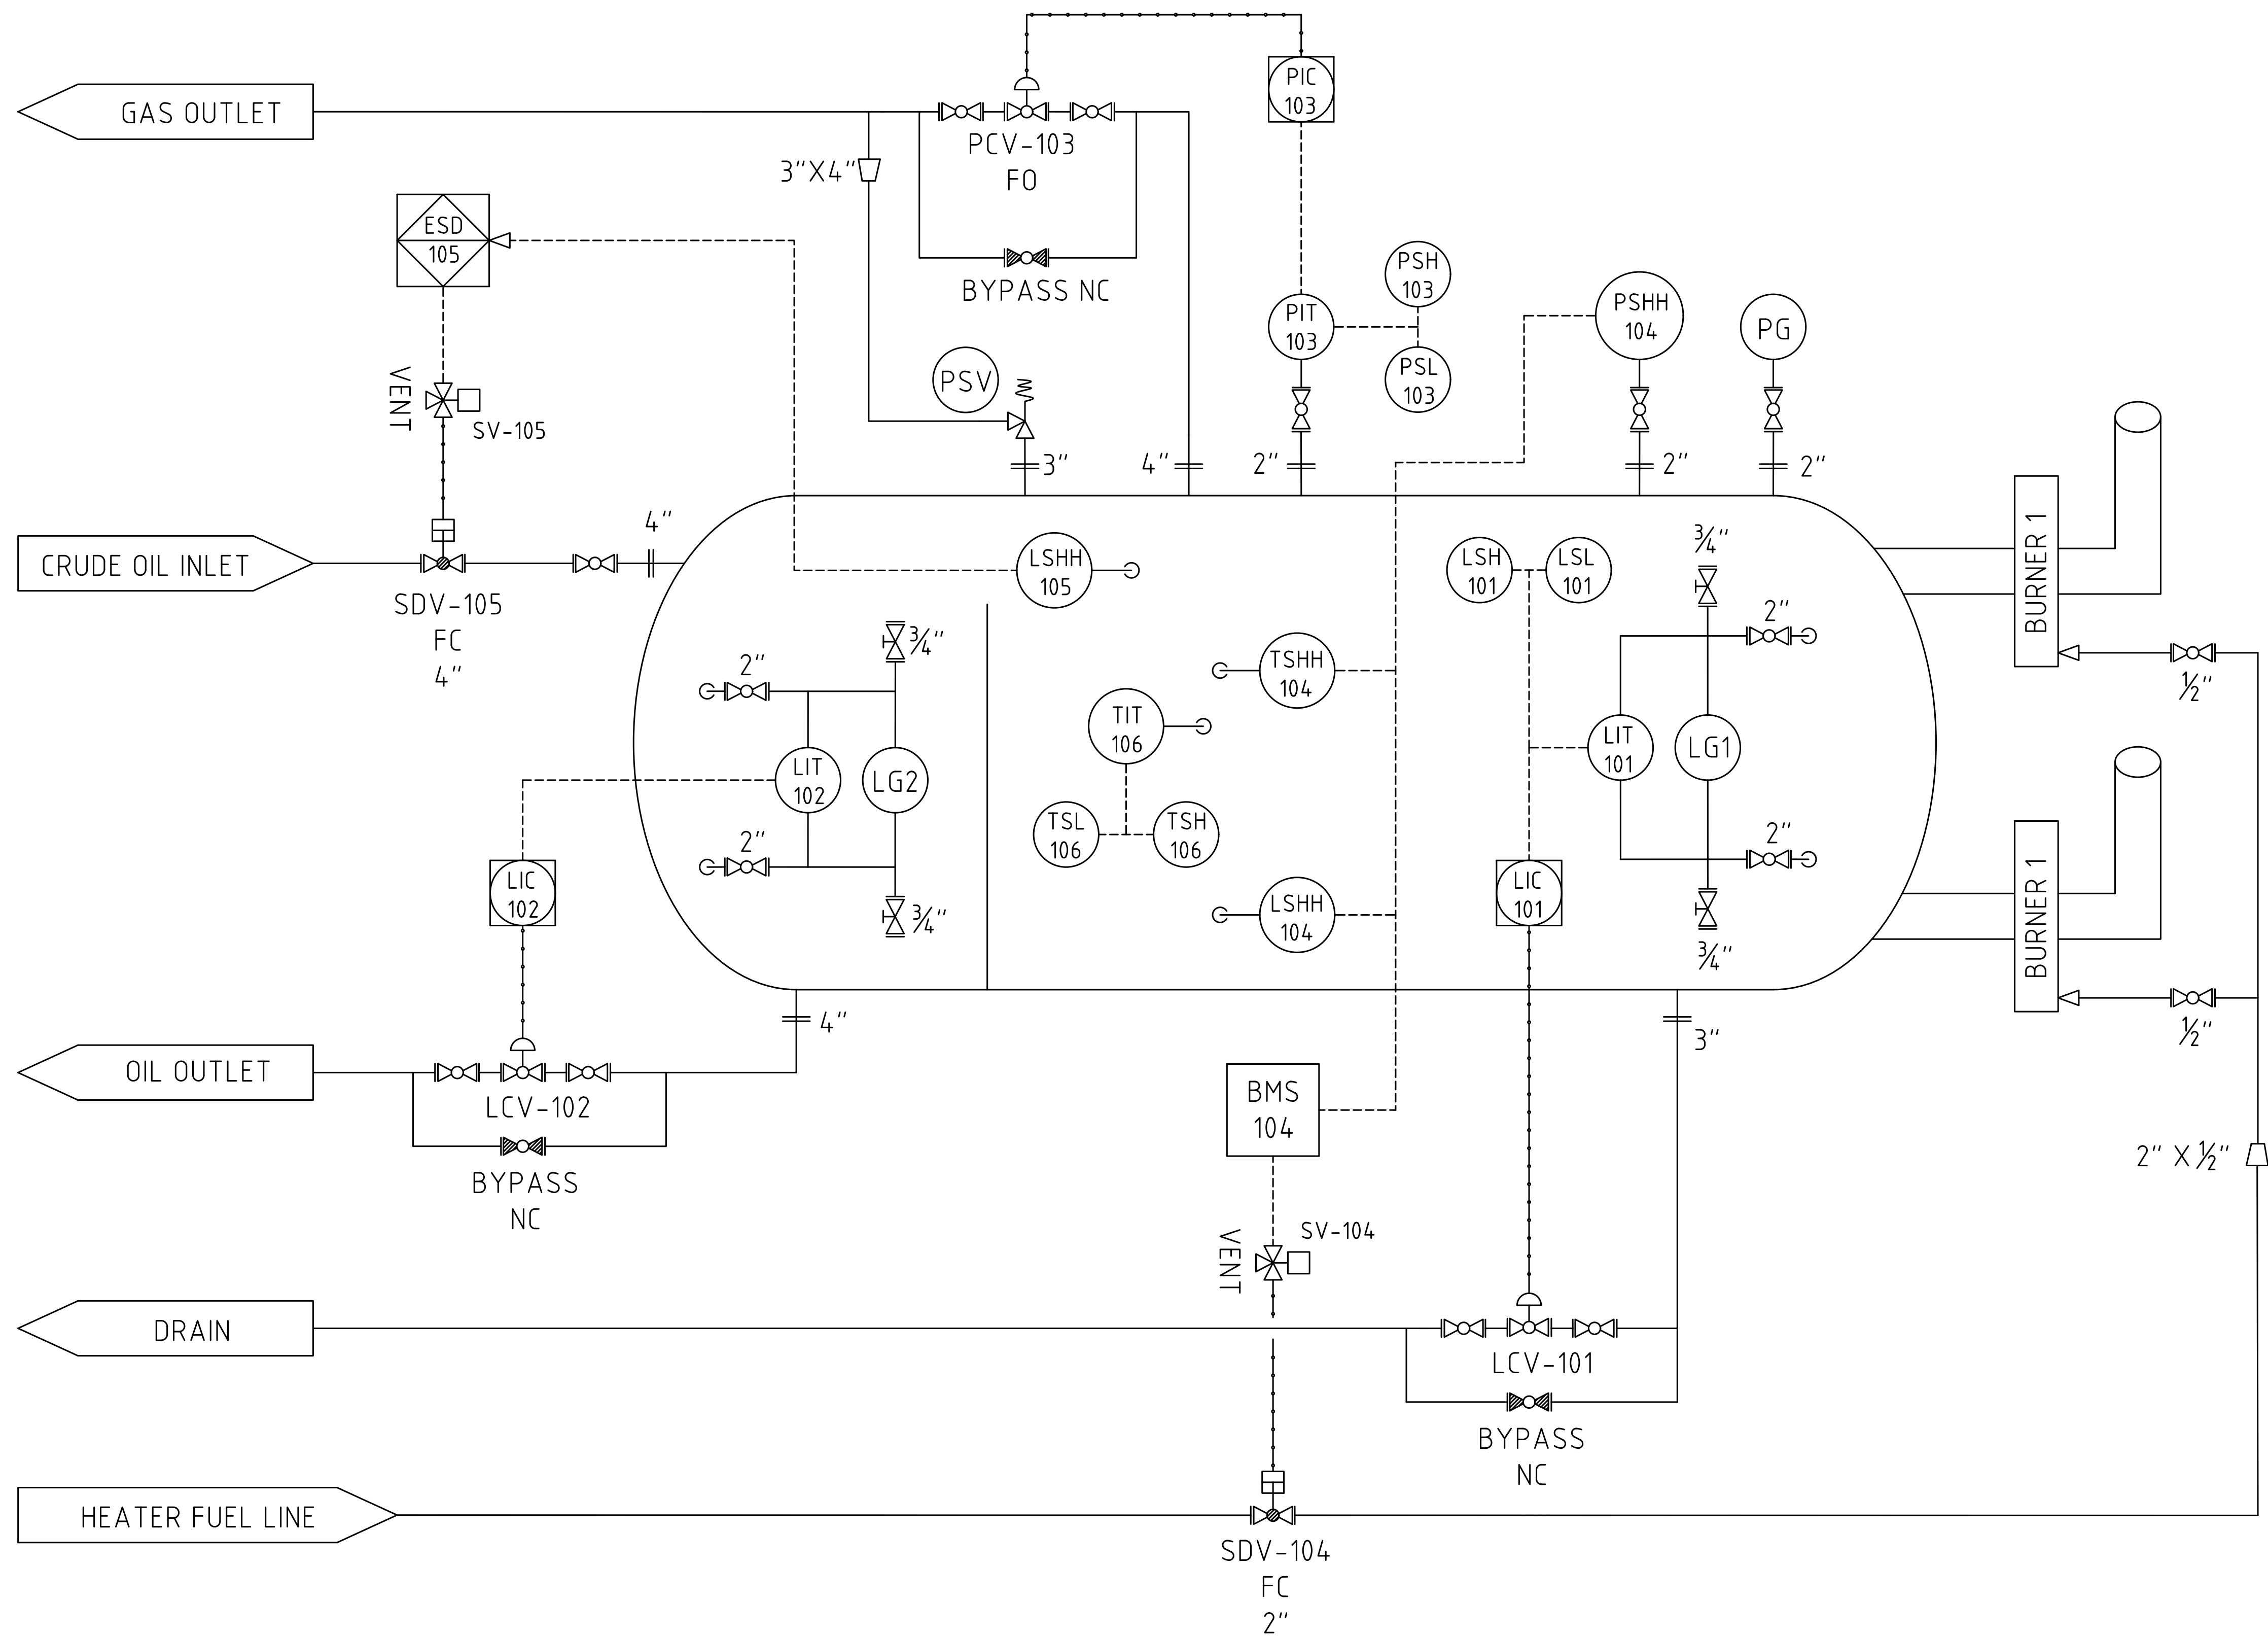

H-101

HT - HEATER TREATER
3.04M OD × 9.5M LENGTH
D/OP DUTY: 4/4 MMBTU/HR
D/OP PRESSURE: 65/ - PSIG
D/OP CAPACITY: 10000/±8000 BPD

SHUTDOWN TRIPS

LSLL-104 — Low-Low Liquid Level
LSHH - 105 — High-High Liquid Level
TSHH-104 — High-High Temperature.
PSHH -104 — High-High Pressure.

PROCESS ALARMS

PSH-103 — High pressure alarm.
PSL-103 — Low pressure alarm.
LSH-102 — High liquid level alarm.
LSL-102 — Low liquid level alarm.
TSH-106 — High temperature.
TSL-106 — High temperature.

VALVES

BALL (SHUTDOWN)	
GLOBE (CONTROL)	
BALL (PNEUMATIC)	
SOLENOID VALVE	
GAUGE COCK	

LINE SYMBOLS:

PROCESS LINE	
SIGNAL LINE	
AIR LINE	

PETROTEC

INDUSTRIAL ENGINEERING COMPANY

DRAWING TITLE

PIPING AND INSTRUMENTATION DIAGRAM
P&ID FOR HEATER TREATER H-101

DWG. NO.	DRAWN BY	DESIGNED BY	DATE
PT-009-03	ENG. I.H	ENG. TAREK HAMMAD	30-May-26

PROPERTY OF PETROTEC. REPRODUCTION OR UNAUTHORIZED USE WITHOUT
PRIOR WRITTEN APPROVAL IS PROHIBITED AND SUBJECT TO LEGAL ACTION.