



DIMS IN MM

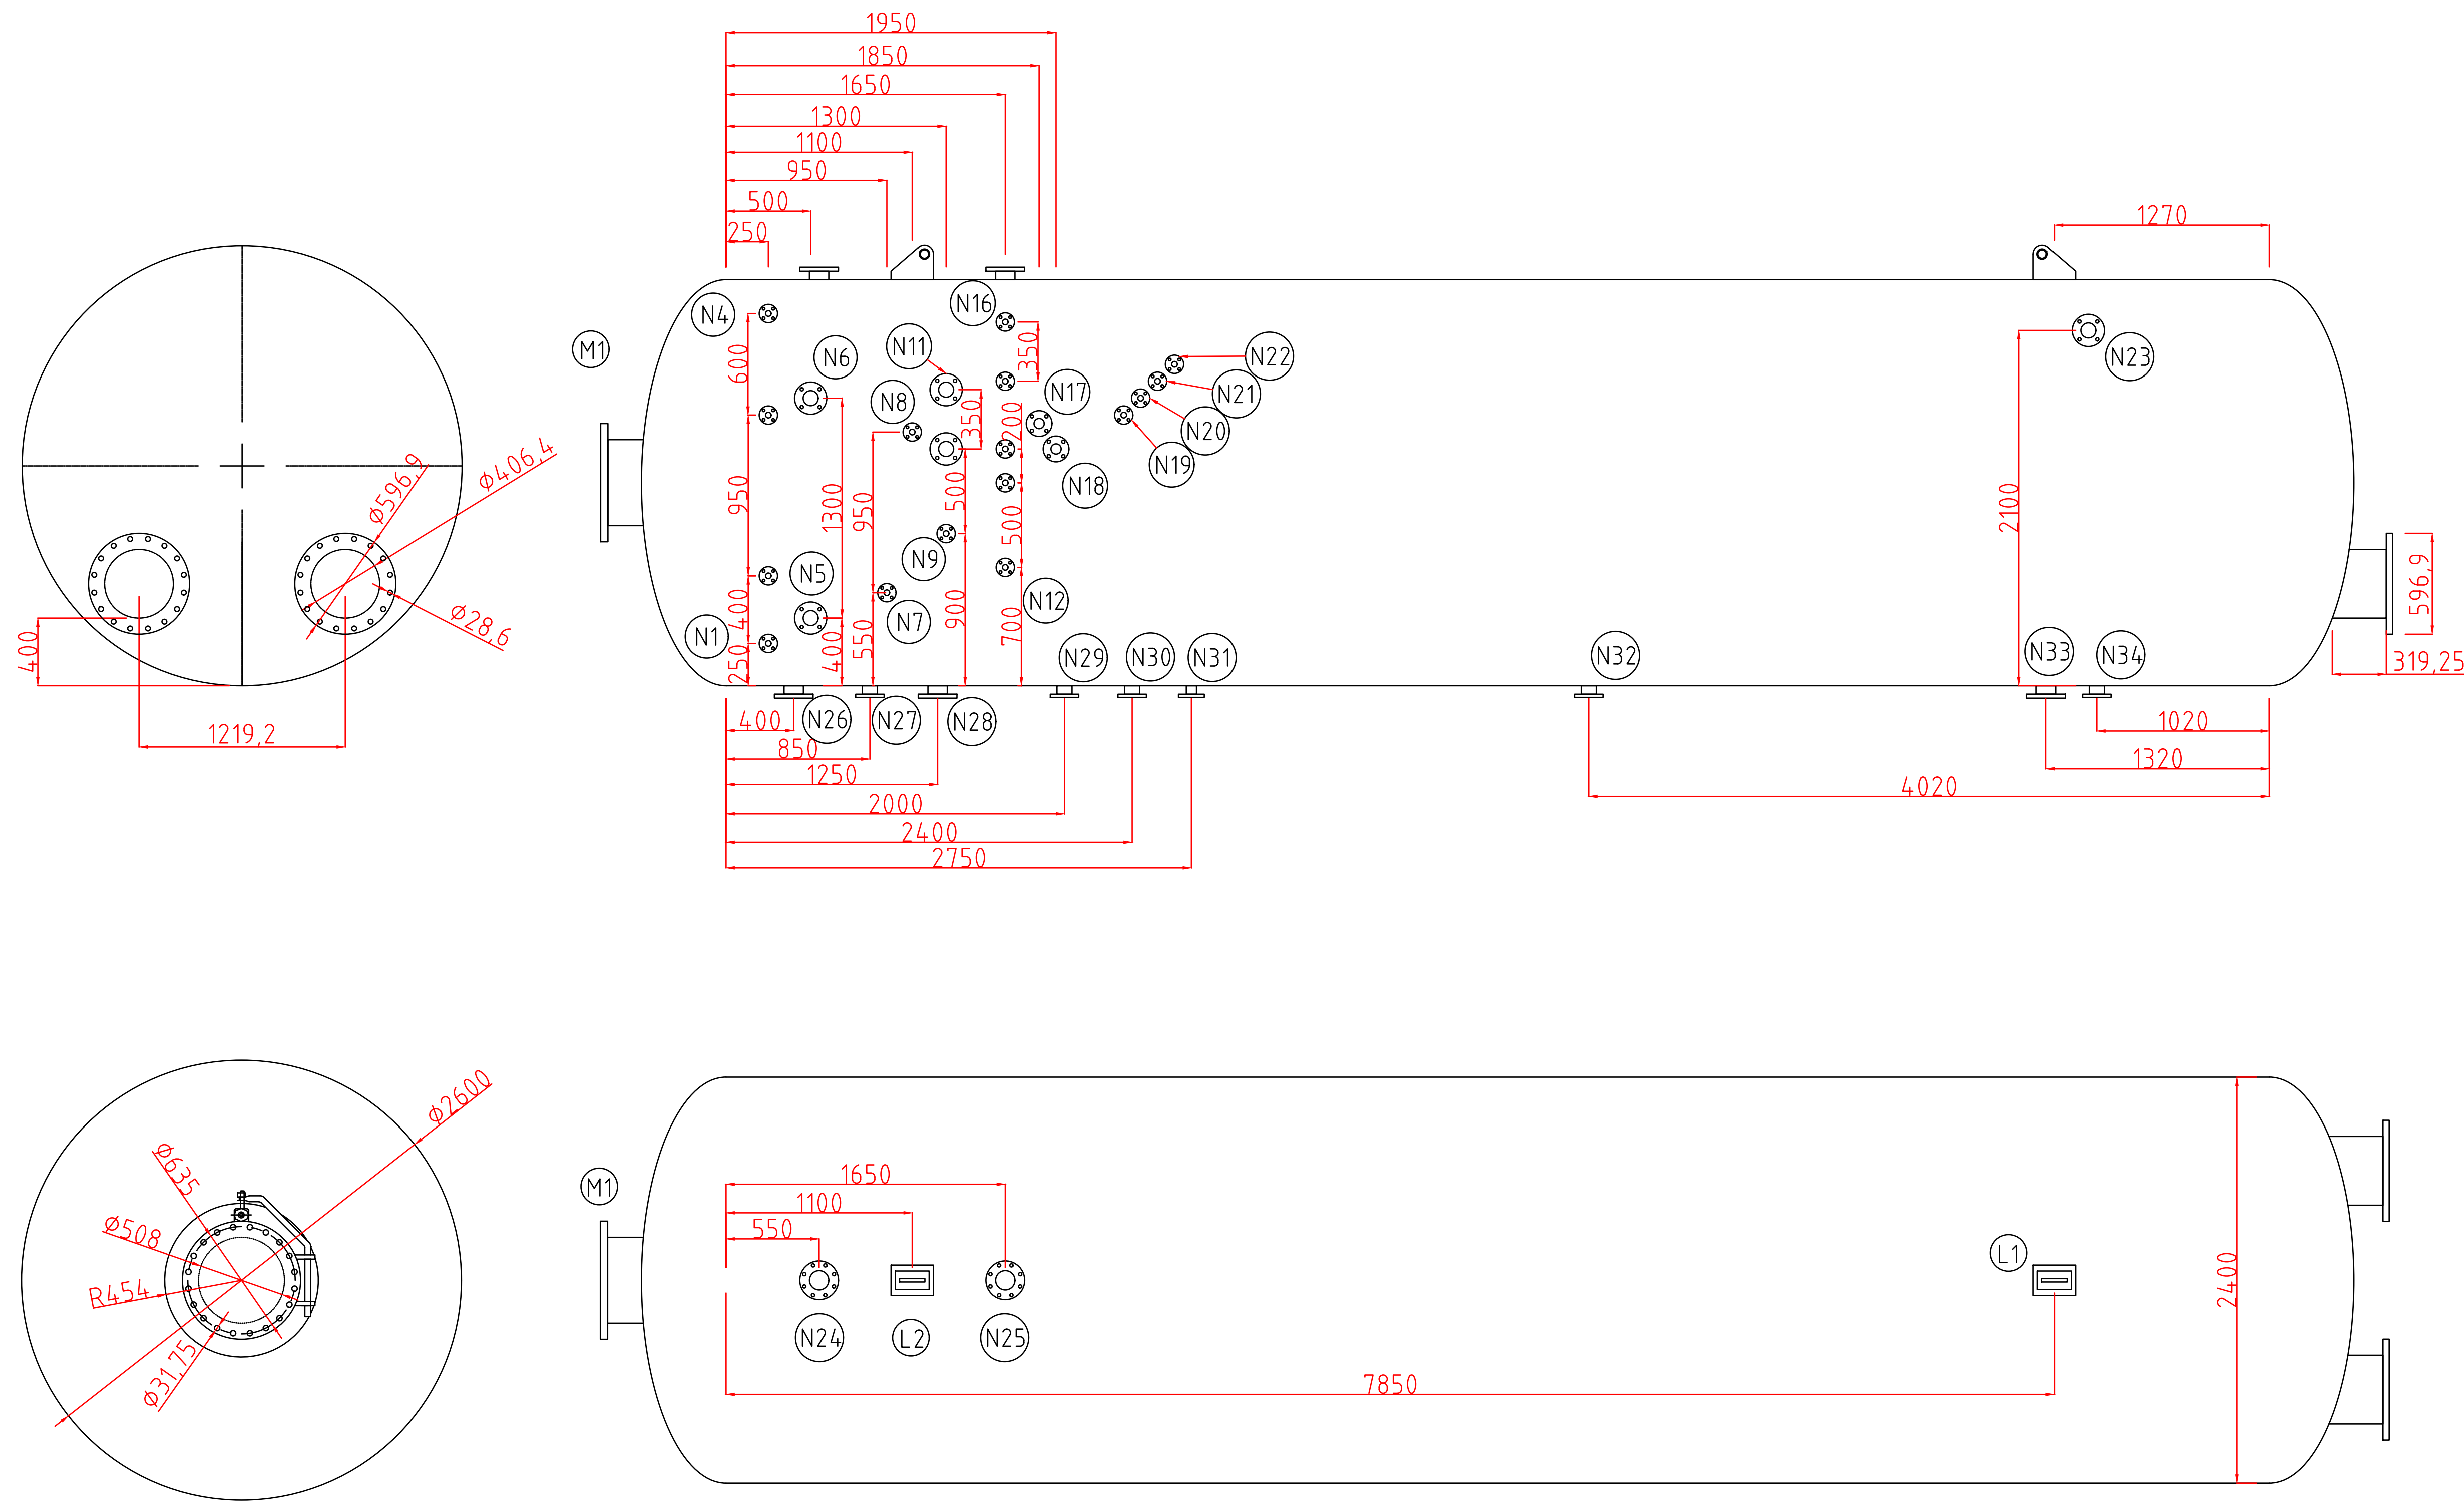

- GENERAL NOTES :
- CODE OF CONSTRUCTION - ASME SEC.VIII-DIV.I-EDD-STAMPED.
 - MAWP: For Shell side=50 psig
 - MDMT=+ 30 F
 - Hydrotest: Shell side=1.3x50=65 psig for duration of 1/2 hour.
 - UW-2 FOR LETHAL SERVICE - NON LETHAL .
 - IMPACT TEST Exempted - UG - 22 (F) , UCS.
 - Stress Releif exempted as per ASME STD.
 - Dimension Tollarence as per ASME SEC VIII.
 - E= 0.60 in Calculation as per ASME STD conditions

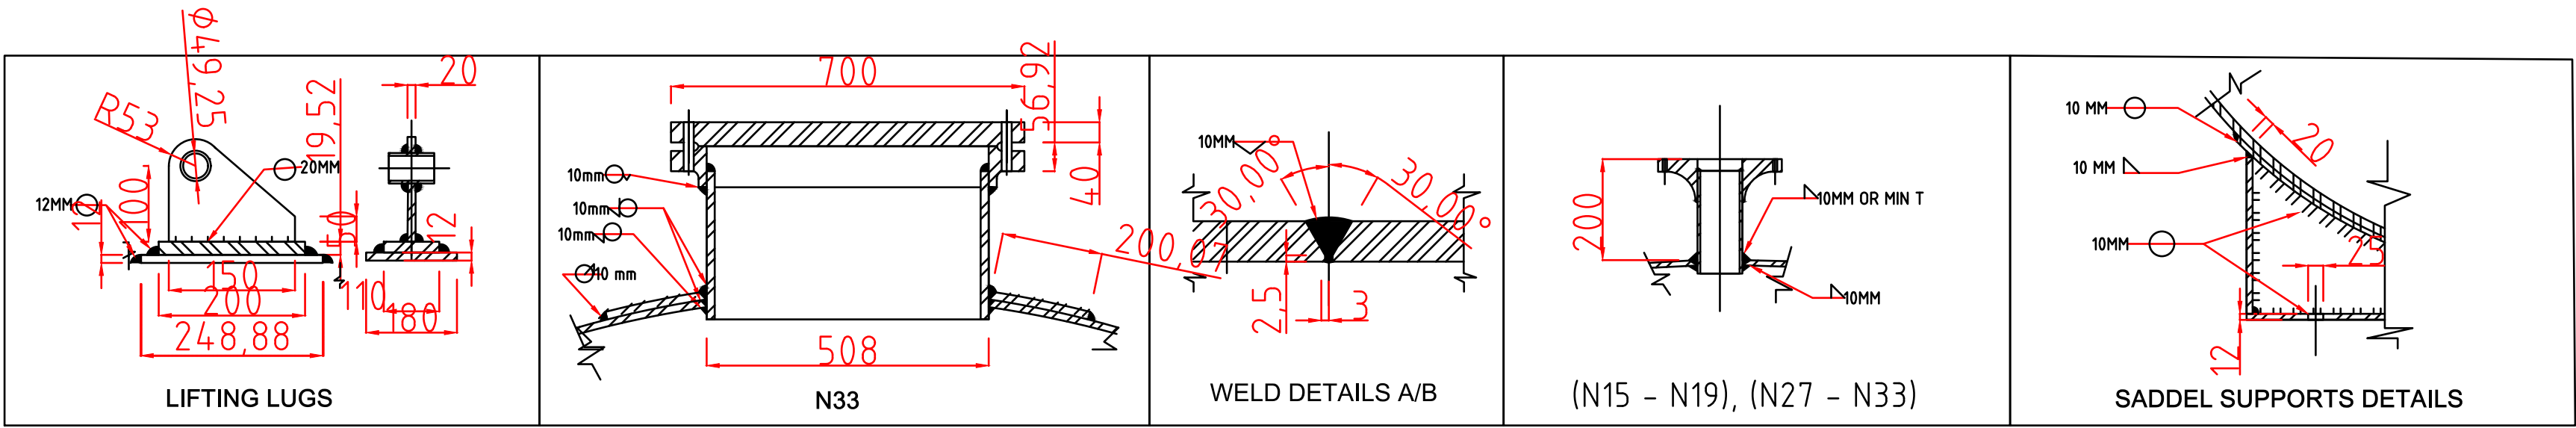

NOZZLE	DIMS/QTY		DESCRIPTION	SPECIFICATION
N1 - N4	1"	4	SIGHT GLASS	SA106-GR.B SA105-B16.5
N5 - N6	3"	2	LEVEL SWITCHES	SA106-GR.B SA105-B16.5
N7 - N9	1"	3	TEMP SENSOR	SA106-GR.B SA105-B16.5
N10	3"	1	LEVEL SWITCHE	SA106-GR.B SA105-B16.5
N11	3"	1	TEMP SENSOR	SA106-GR.B SA105-B16.5
N12 - N16	1"	5	SIGHT GLASS	SA106-GR.B SA105-B16.5
N17 - N18	2"	2	OIL/WATER SENSOR	SA106-GR.B SA105-B16.5
N19 - N22	1"	4	SAMPLING NOZZLE	SA106-GR.B SA105-B16.5
N23	2"	1	LEVEL SWITCH	SA106-GR.B SA105-B16.5
N24 - N25	4"	2	GAS OUTLET	SA106-GR.B SA105-B16.5
N26	4"	1	OIL OUTLET	SA106-GR.B SA105-B16.5
N27, N29, N30, N32	3"	4	WATER DRAIN	SA106-GR.B SA105-B16.5
N28, N33	4"	2	WATER DRAIN	SA106-GR.B SA105-B16.5
N31	2"	1	WATER RECYCLE	SA106-GR.B SA105-B16.5
N34	3"	1	FRESH WATER INLET	SA106-GR.B SA105-B16.5
M1	20"	1	MANHOLE	SA516-GR.70 SA105-B16.5
L1 - L2	-	2	LIFTING LUGS	SA516-GR.70 SA105-B16.5


PETROTEC

INDUSTRIAL ENGINEERING COMPANY

HEATER TREATER

GENERAL ASEMBLY - MECHANICAL DETAILS

VESSEL MATERIAL	VESSEL THICKNESS	LENGTH	DIAMETER	SERIAL NO.
SA-283 Grade C	8MM	9.12M	2.4M	PT-00410
ENDCAP MATERIAL	ENDCAP THICKNESS	ENDCAP TYPE	TOTAL WEIGHT	
SA-283 Grade C	8MM	ELLIPTICAL	15 TON	
DWG. NO.	DRAWN BY	DESIGNED BY	REV.	DATE
PT-410-01	ENG. I.H	ENG. TAREK HAMMAD	01	04-May-26

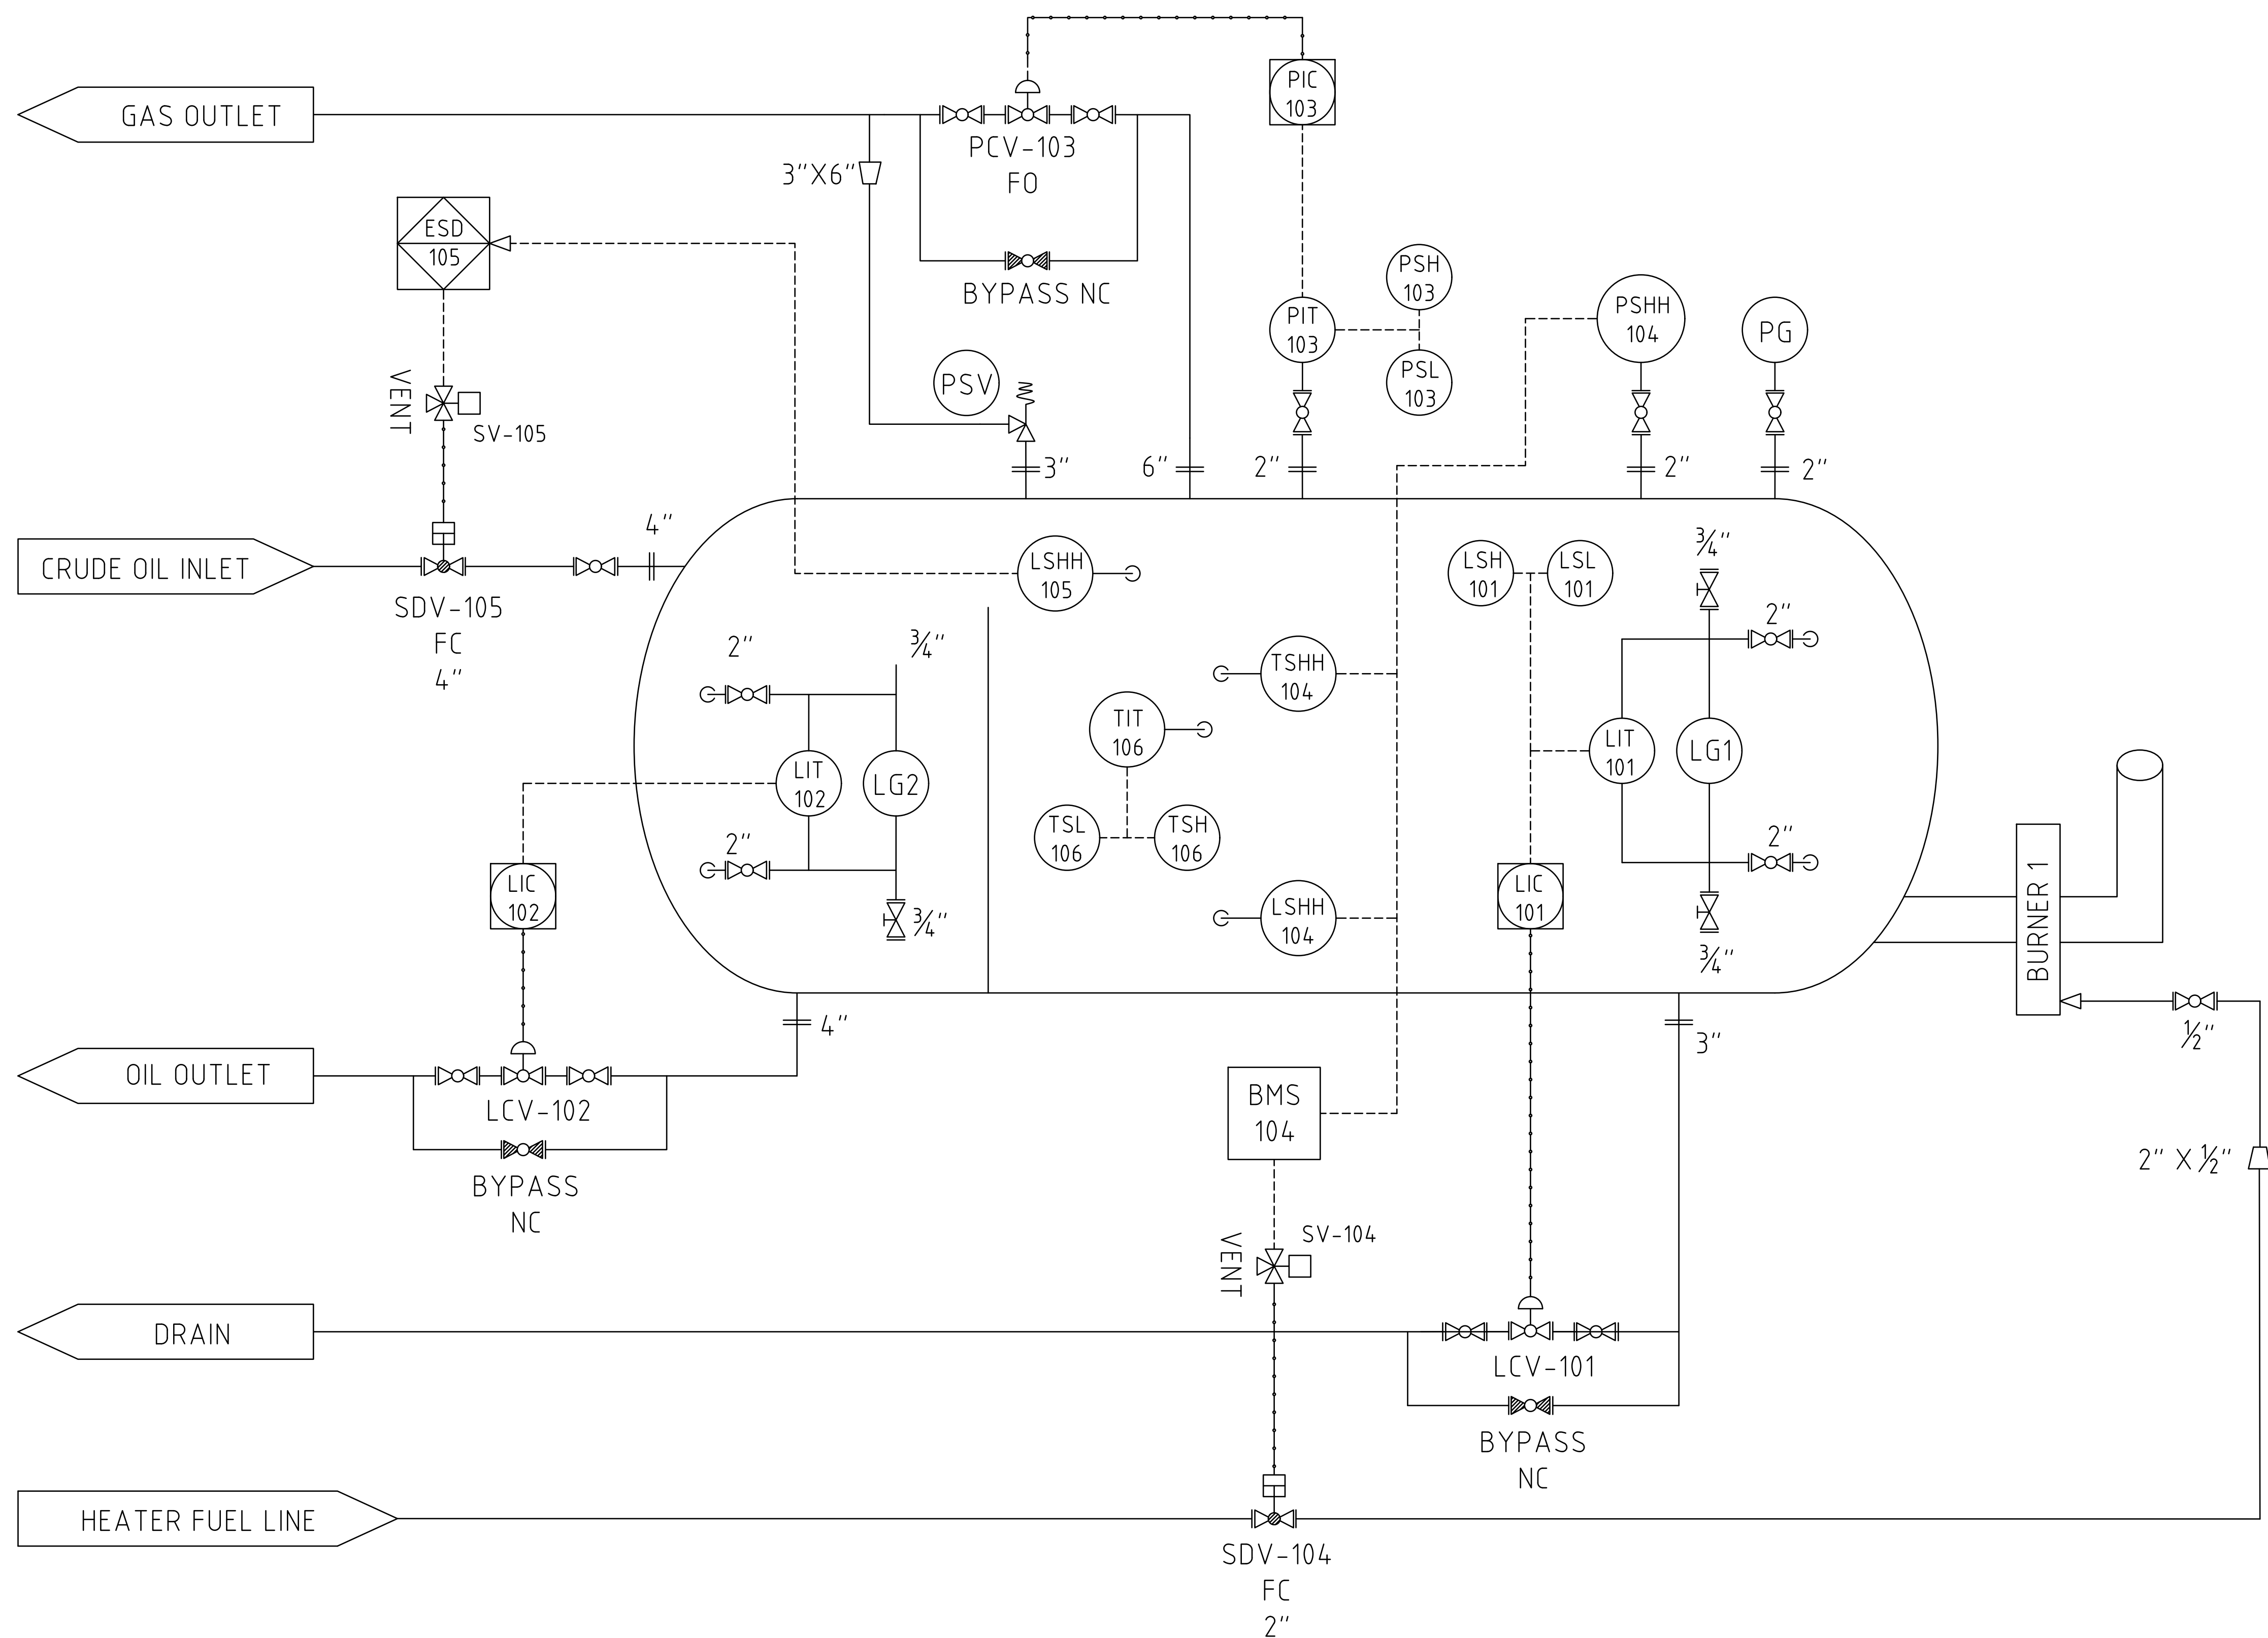

H-101

HT - HEATER TREATER
2.4M OD × 9.12M LENGTH
D/OP DUTY: 6/6 MMBTU/HR
D/OP PRESSURE: 50/ - PSIG
D/OP CAPACITY: 9000/±5000 BPD




SHUTDOWN TRIPS

LSLL-104 — Low-Low Liquid Level
TSHH-104 — High-High Temperature.
PSHH -104 — High-High Pressure.
LSHH - 105 — High-High Liquid Level (INLET)

PROCESS ALARMS

PSH-103 — High pressure alarm.
PSL-103 — Low pressure alarm.
LSH-102 — High liquid level alarm.
LSL-102 — Low liquid level alarm.
TSH-106 — High temperature.
TSL-106 — High temperature.

VALVES

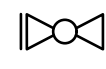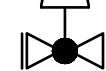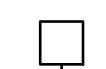BALL (SHUTDOWN) 
GLOBE (CONTROL) 
BALL (PNEUMATIC) 
SOLENOID VALVE 
GAUGE COCK 

LINE SYMBOLS:

PROCESS LINE 
SIGNAL LINE 
AIR LINE 

PETROTEC

INDUSTRIAL ENGINEERING COMPANY

DRAWING TITLE

PIPING AND INSTRUMENTATION DIAGRAM
P&ID FOR HEATER TREATER H-101

DWG. NO.	DRAWN BY	DESIGNED BY	DATE
PT-410-03	ENG. I.H	ENG. TAREK HAMMAD	30-May-26

PROPERTY OF PETROTEC. REPRODUCTION OR UNAUTHORIZED USE WITHOUT
PRIOR WRITTEN APPROVAL IS PROHIBITED AND SUBJECT TO LEGAL ACTION.