


1. CODE OF CONSTRUCTION -ASME SEC.VIII-DIV.I-EDD-STAMPED.
2. MAWP: For Shell side=50 psig
3. MDMT=+ 30 F
4. Hydrotest: Shell side=1.3x50=65 psig
for duration of 1/2 hour.
5. UW-2 FOR LETHAL SERVICE - NON LETHAL .
6. IMPACT TEST Exempted - UG - 22 (F) , UCS.
7. Stress Releif exempted as per ASME STD.
8. Dimension Tollarence as per ASME SEC VIII.
9. E= 0.60 in Calculation as per ASME STD conditions

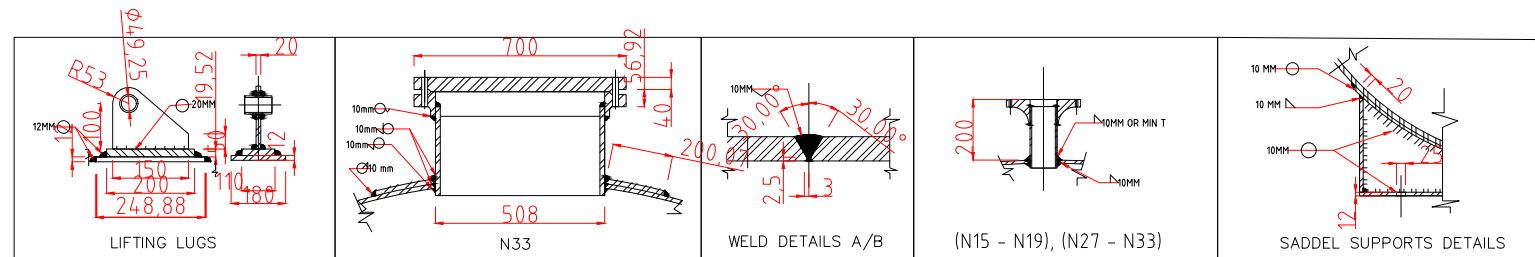

NOZZLE	DIMS/ QTY		DESCRIPTION	SPECIFICATION
N1 - N4, N13 - N17, N19 - N20	1"	11	SIGHT GLASS	SA106-GR.B SA105-B16.5
N5, N6, N9 N12, N21	3"	5	LEVEL SWITCHES	SA106-GR.B SA105-B16.5
N7, N8, N10	2"	3	OIL/WATER SENSOR	SA106-GR.B SA105-B16.5
N11, N18	1"	2	TEMPERATURE TRANSMITTER	SA106-GR.B SA105-B16.5
N22 - N23	2"	2	OIL/WATER SENSOR	SA106-GR.B SA105-B16.5
N24 - N28	1"	4	SAMPLING NOZZLE	SA106-GR.B SA105-B16.5
N29	3"	1	LEVEL SWITCH	SA106-GR.B SA105-B16.5
N30 - N31	3"	2	GAS OUTLET	SA106-GR.B SA105-B16.5
N32	2"	1	PRESSURE GAUGE	SA106-GR.B SA105-B16.5
N33 - N34	6"	2	PRESSURE SAFETY VALVE	SA106-GR.B SA105-B16.5
L1 - L2	-	2	LIFTING LUGS	SA516-GR.70 SA105-B16.5
N35, N37	2"	2	WATER DRAIN	SA106-GR.B SA105-B16.5
N36	4"	1	OIL OUTLET	SA106-GR.B SA105-B16.5
N38 - N39	3"	2	WATER DRAIN	SA106-GR.B SA105-B16.5
N40	4"	1	CRUDE OIL INPUT	SA106-GR.B SA105-B16.5
N41	2"	1	FRESH WATER INLET	SA106-GR.B SA105-B16.5
M1 - M2	20"	2	MANHOLE	SA516-GR.70 SA105-B16.5

INDUSTRIAL ENGINEERING COMPANY

GENERAL ASSEMBLY - MECHANICAL DETAILS

VESSEL MATERIAL	VESSEL THICKNESS	LENGTH	DIAMETER	SERIAL NO.
SA-283 Grade C	8MM	9.12M	2.4M	PT-00411
ENDCAP MATERIAL	ENDCAP THICKNESS	ENDCAP TYPE	TOTAL WEIGHT	
SA-283 Grade C	8MM	ELLIPTICAL	15 TON	
DWG. NO.	DRAWN BY	DESIGNED BY	REV.	DATE
PT-026-3	ENG. I.H	ENG. TAREK HAMMAD	03	04-May-26

PROPERTY OF PETROTEC. REPRODUCTION OR UNAUTHORIZED USE WITHOUT PRIOR WRITTEN APPROVAL IS PROHIBITED AND SUBJECT TO LEGAL ACTION.