


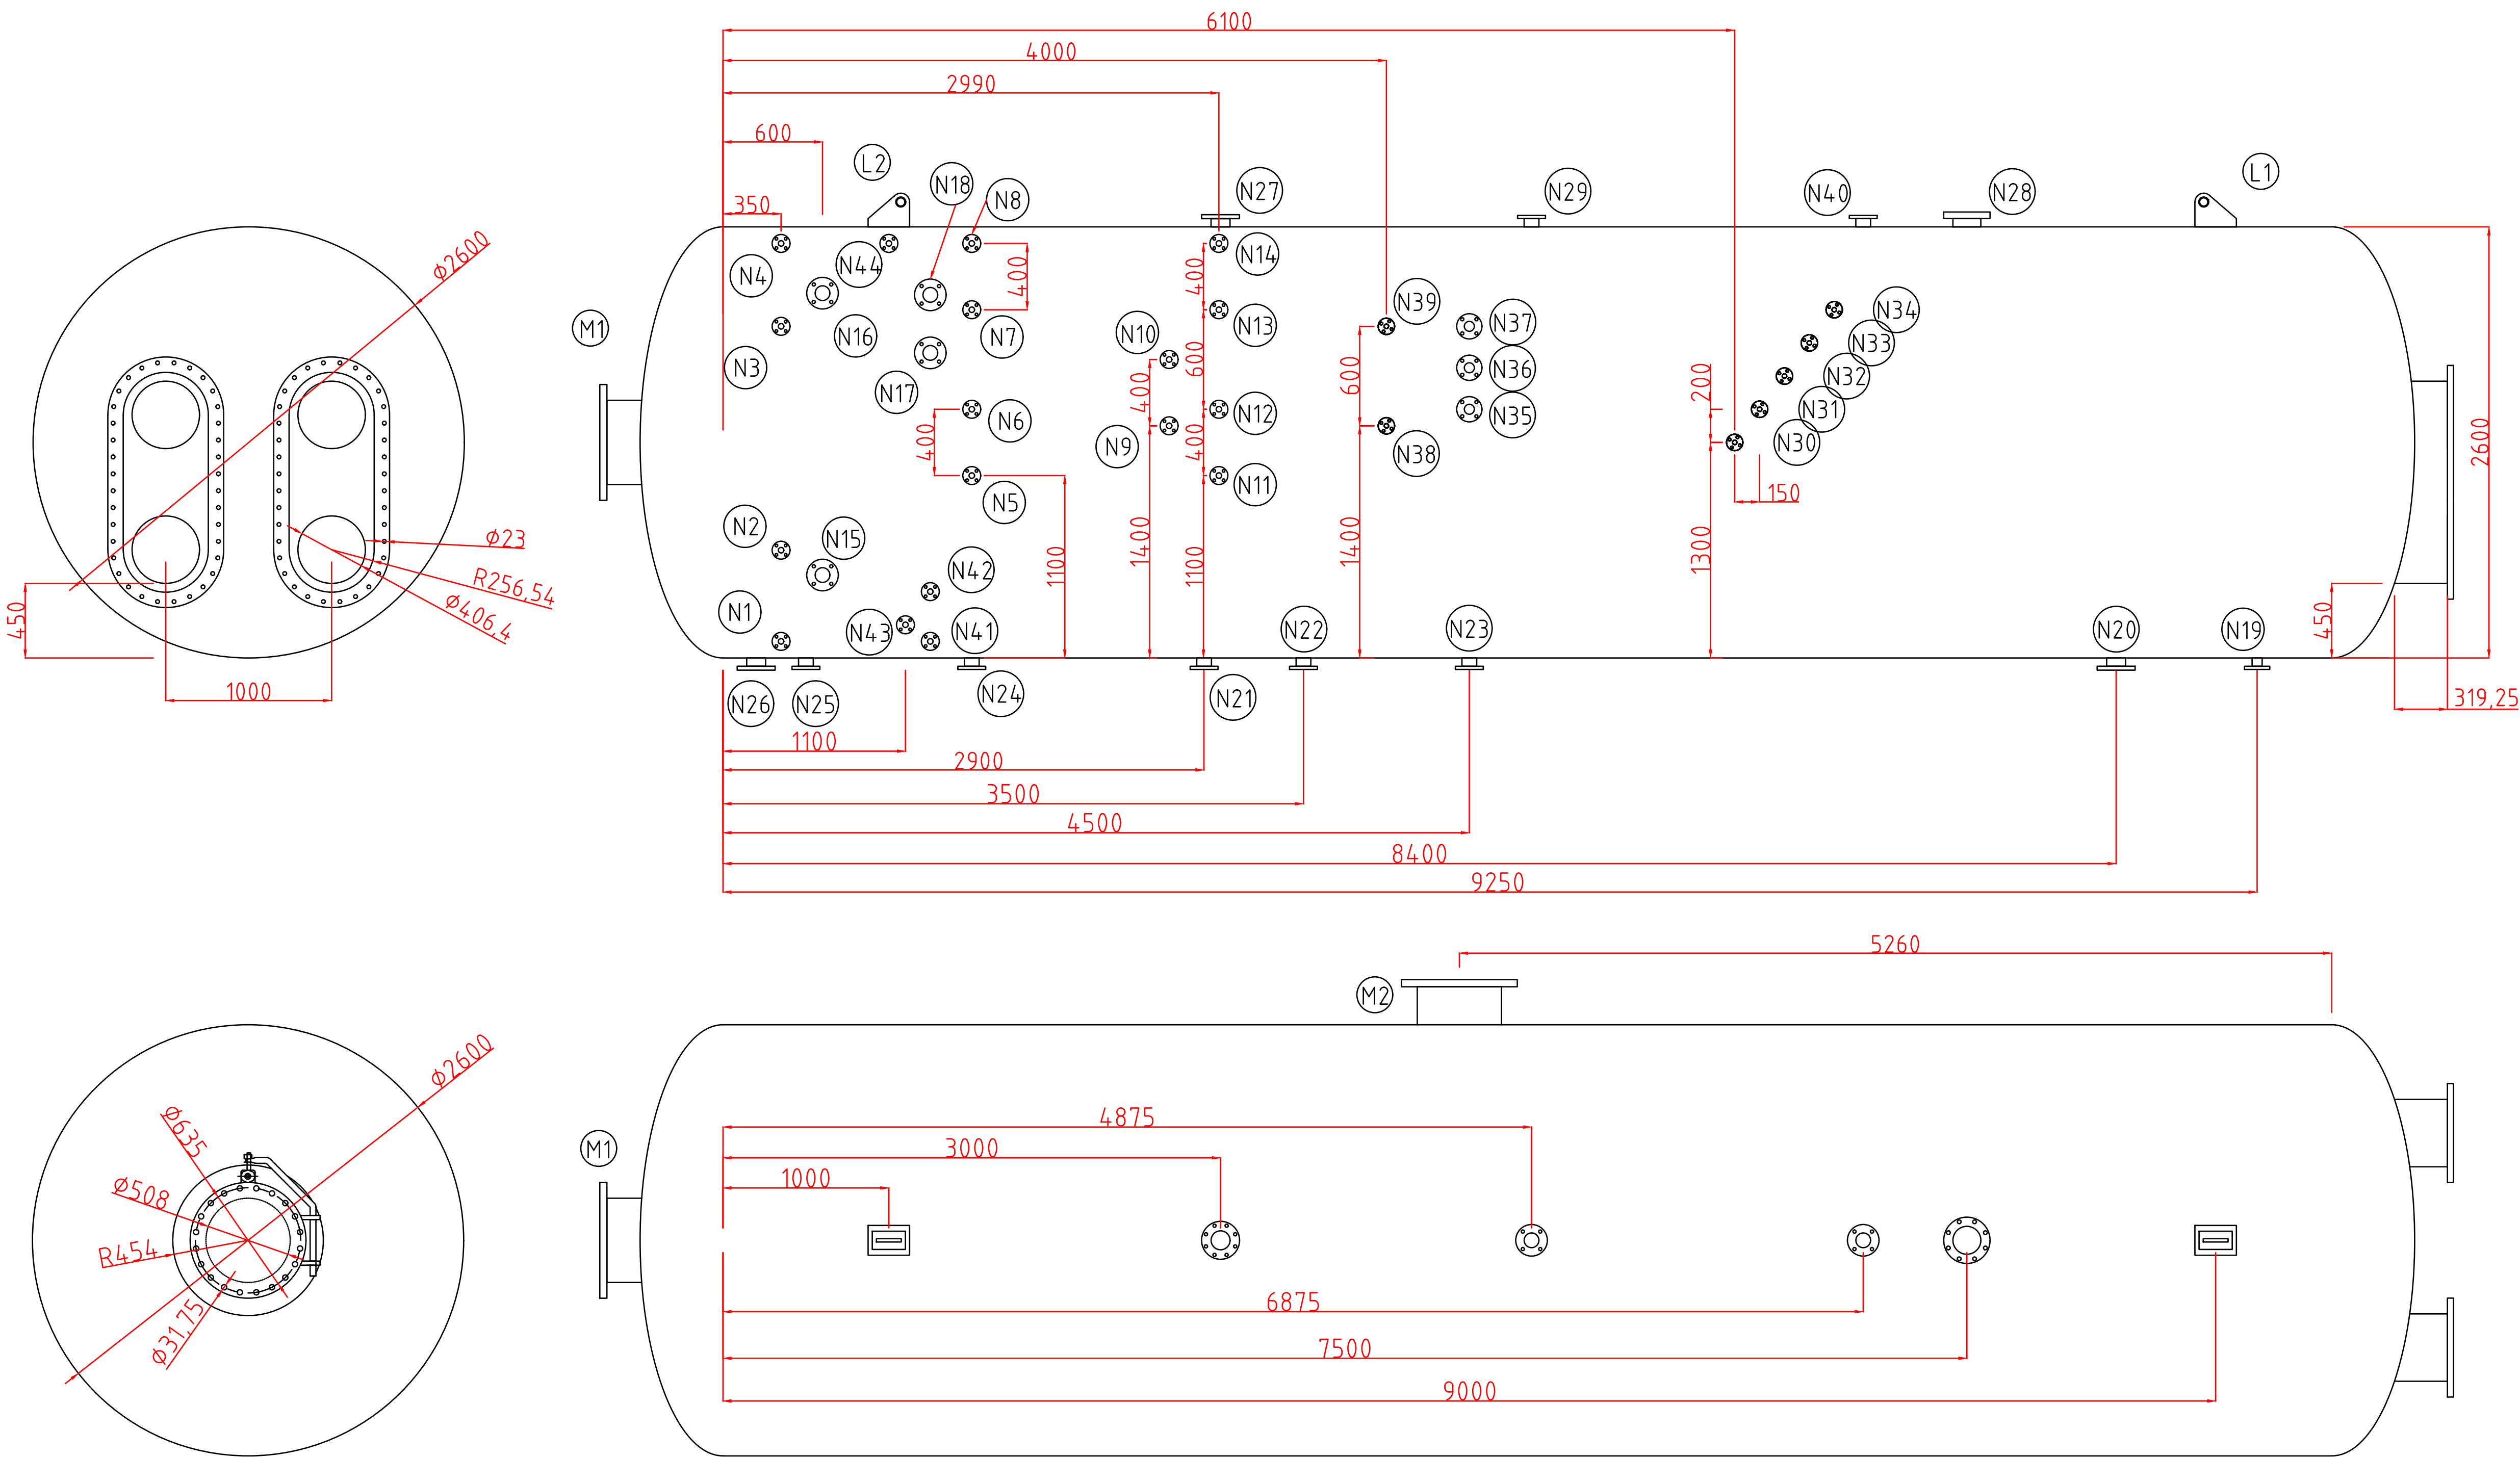

DIMS IN MM

NOZZLE	DIMS/ QTY		DESCRIPTION	SPECIFICATION
N1 - N14	1"	14	SIGHT GLASS	SA106-GR.B SA105-B16.5
N15 - N18	3"	4	LEVEL SWITCHES	SA106-GR.B SA105-B16.5
N19	2"	1	FRESH WATER INLET	SA106-GR.B SA105-B16.5
N20	4"	1	CRUDE OIL INPUT	SA106-GR.B SA105-B16.5
N21 - N23	3"	3	WATER DRAIN	SA106-GR.B SA105-B16.5
N24 - N25	3"	2	OIL DRAIN	SA106-GR.B SA105-B16.5
N26	4"	1	OIL OUTLET	SA106-GR.B SA105-B16.5
N27	6"	1	GAS OUTLET	SA106-GR.B SA105-B16.5
N28	4"	1	GAS OUTLET	SA106-GR.B SA105-B16.5
N29	3"	1	GAS OUTLET	SA106-GR.B SA105-B16.5
N30 - N34	3/4"	5	SAMPLING NOZZLE	SA106-GR.B SA105-B16.5
N35 - N37	2"	3	OIL/WATER SENSOR	SA106-GR.B SA105-B16.5
N38 - N39	3/4"	2	TEMPERATURE TRANSMITTER	SA106-GR.B SA105-B16.5
N40	3"	1	2ND STAGE	SA106-GR.B SA105-B16.5
N41 - N43	1"	3	SENSORS	SA106-GR.B SA105-B16.5
N44	1"	1	PRESSURE GAUGE	SA106-GR.B SA105-B16.5
L1 - L2	-	2	LIFTING LUGS	SA516-GR.70 SA105-B16.5
M1 - M2	20"	2	MANHOLE	SA516-GR.70 SA105-B16.5

PETROTEC

INDUSTRIAL ENGINEERING COMPANY

HEATER TREATER

GENERAL ASSEMBLY - MECHANICAL DETAILS

VESSEL MATERIAL	VESSEL THICKNESS	LENGTH	DIAMETER	SERIAL NO.
SA-283 Grade C	8MM	9.7M	2.6M	PT-00412
ENDCAP MATERIAL	ENDCAP THICKNESS	ENDCAP TYPE	TOTAL WEIGHT	
SA-283 Grade C	8MM	ELLIPTICAL	16 TON	
DWG. NO.	DRAWN BY	DESIGNED BY	REV.	DATE
PT-412-01	ENG. I.H	ENG. TAREK HAMMAD	02	04-May-26

- GENERAL NOTES :
- CODE OF CONSTRUCTION -ASME SEC.VIII-DIV.I-EDD-STAMPED.
 - MAWP: For Shell side=50 psig
 - MDMT=+ 30 F
 - Hydrotest: Shell side=1.3x50=65 psig for duration of 1/2 hour.
 - UW-2 FOR LETHAL SERVICE - NON LETHAL .
 - IMPACT TEST Exempted - UG - 22 (F) , UCS.
 - Stress Releif exempted as per ASME STD.
 - Dimension Tollarence as per ASME SEC VIII.
 - E= 0.60 in Calculation as per ASME STD conditions

