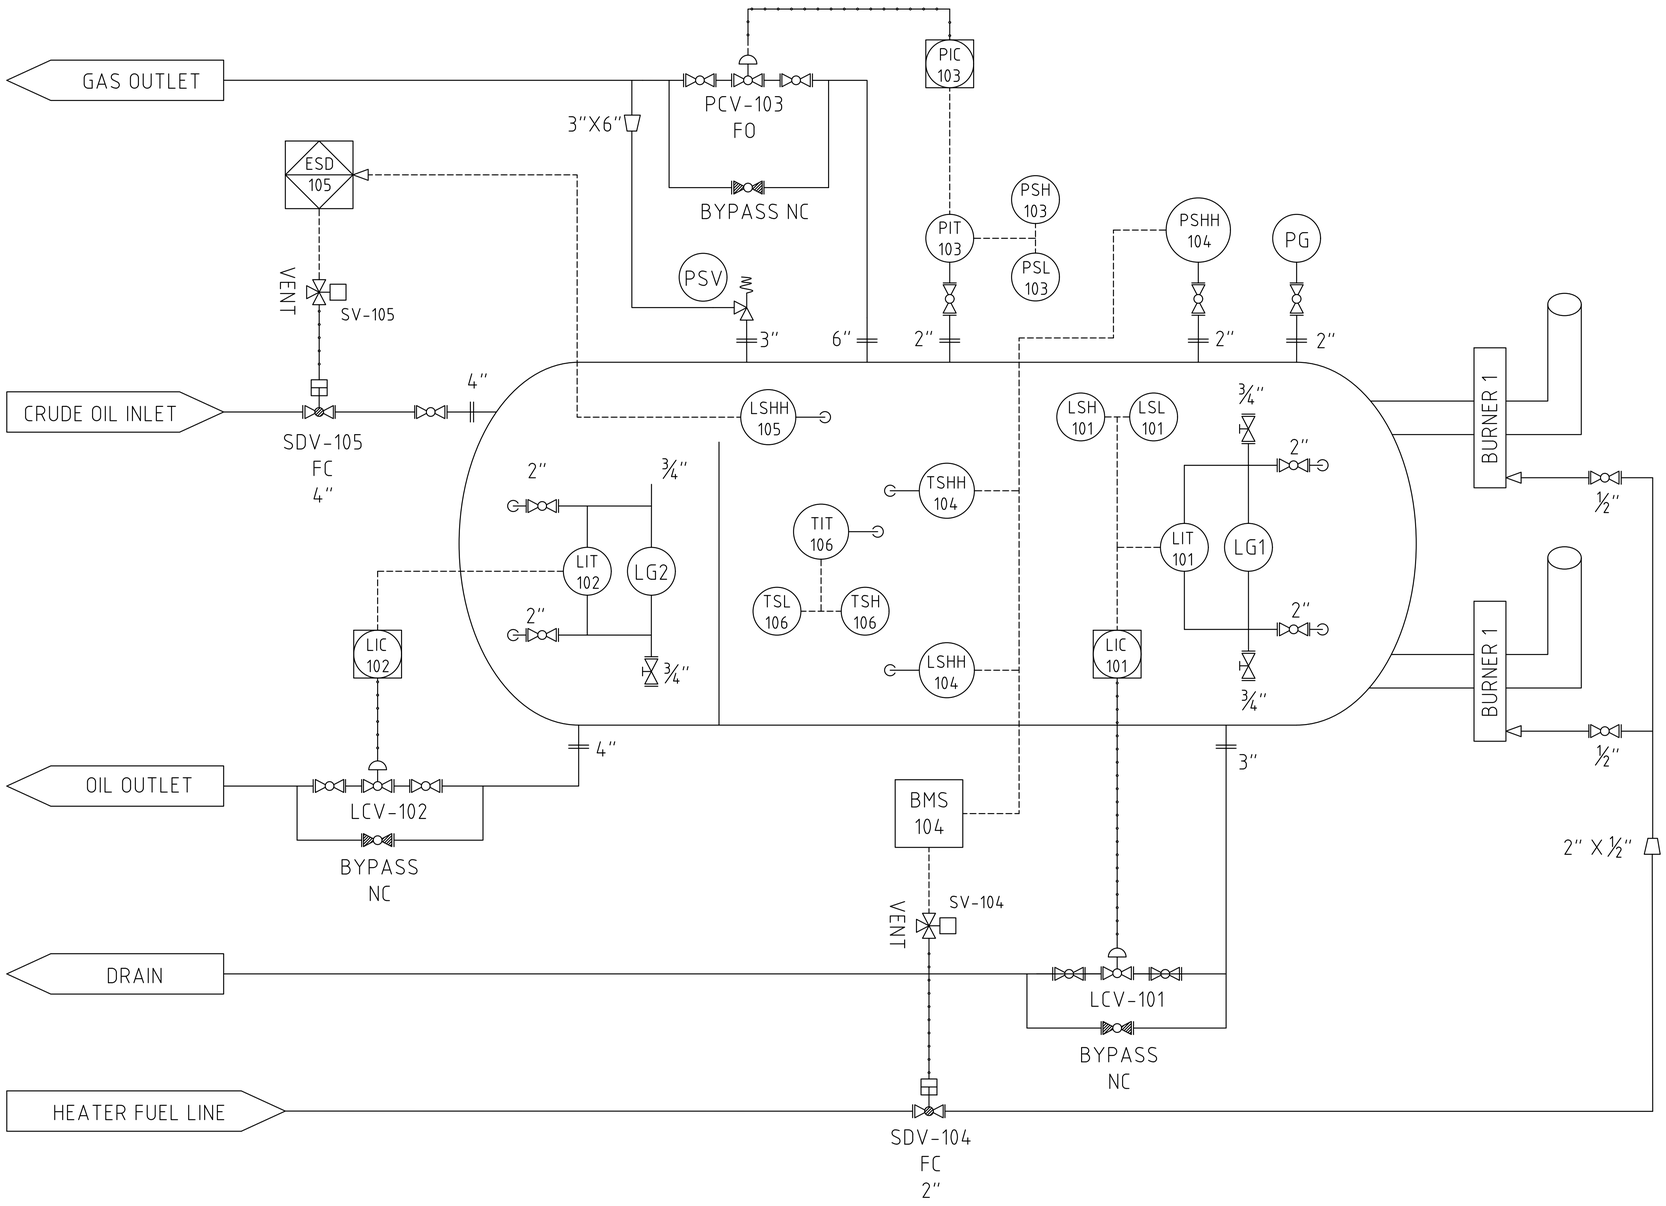


H-101

HT - HEATER TREATER
2.6M OD × 9.7M LENGTH
D/OP DUTY: 8/8 MMBTU/HR
D/OP PRESSURE: 60/ - PSIG
D/OP CAPACITY: 10000/±7000 BPD

SHUTDOWN TRIPS

LSLL-104 — Low-Low Liquid Level
TSHH-104 — High-High Temperature.
PSHH -104 — High-High Pressure.
LSHH - 105 — High-High Liquid Level (INLET)

PROCESS ALARMS

PSH-103 — High pressure alarm.
PSL-103 — Low pressure alarm.
LSH-102 — High liquid level alarm.
LSL-102 — Low liquid level alarm.
TSH-106 — High temperature.
TSL-106 — High temperature.

VALVES

BALL (SHUTDOWN)
GLOBE (CONTROL)
BALL (PNEUMATIC)
SOLENOID VALVE
GAUGE COCK

LINE SYMBOLS:

PROCESS LINE
SIGNAL LINE
AIR LINE

PETROTEC

INDUSTRIAL ENGINEERING COMPANY

DRAWING TITLE

PIPING AND INSTRUMENTATION DIAGRAM
P&ID FOR HEATER TREATER H-101

DWG. NO.	DRAWN BY	DESIGNED BY	DATE
PT-412-03	ENG. I.H	ENG. TAREK HAMMAD	30-May-26

PROPERTY OF PETROTEC. REPRODUCTION OR UNAUTHORIZED USE WITHOUT PRIOR WRITTEN APPROVAL IS PROHIBITED AND SUBJECT TO LEGAL ACTION.