




SIDE VIEW B-B

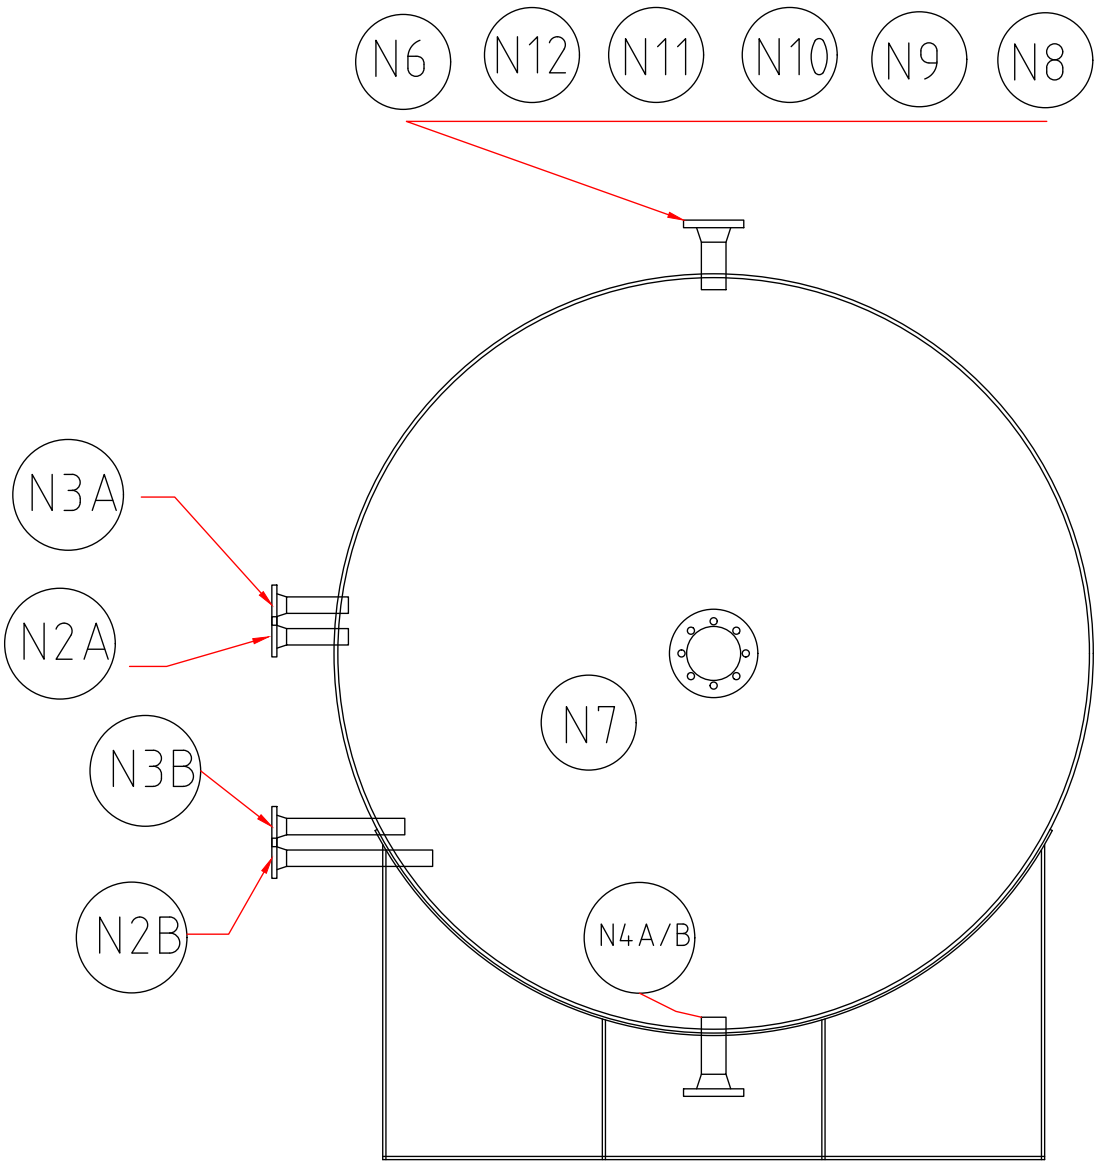



SIDE VIEW C-C

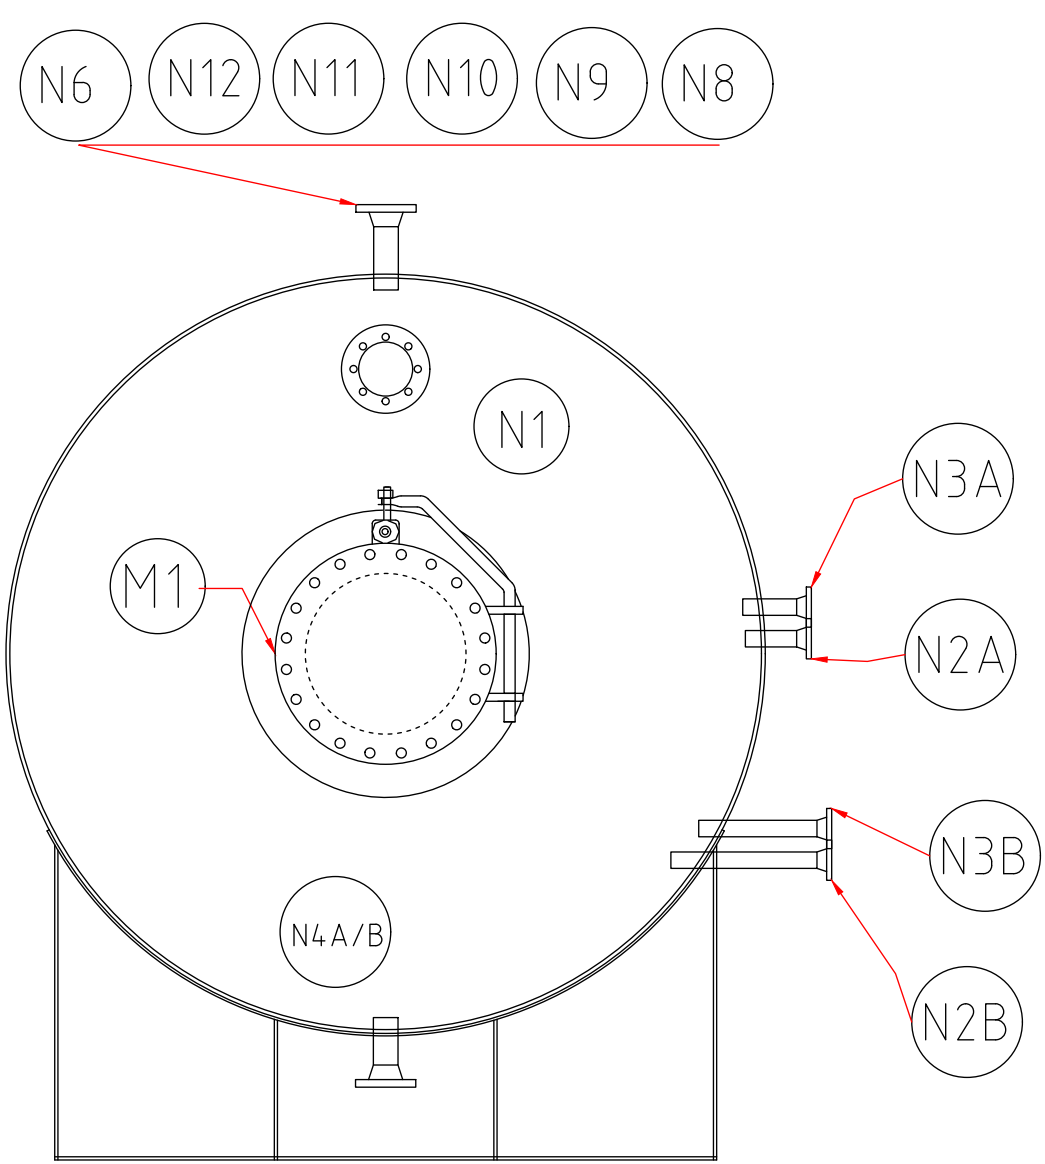


W1

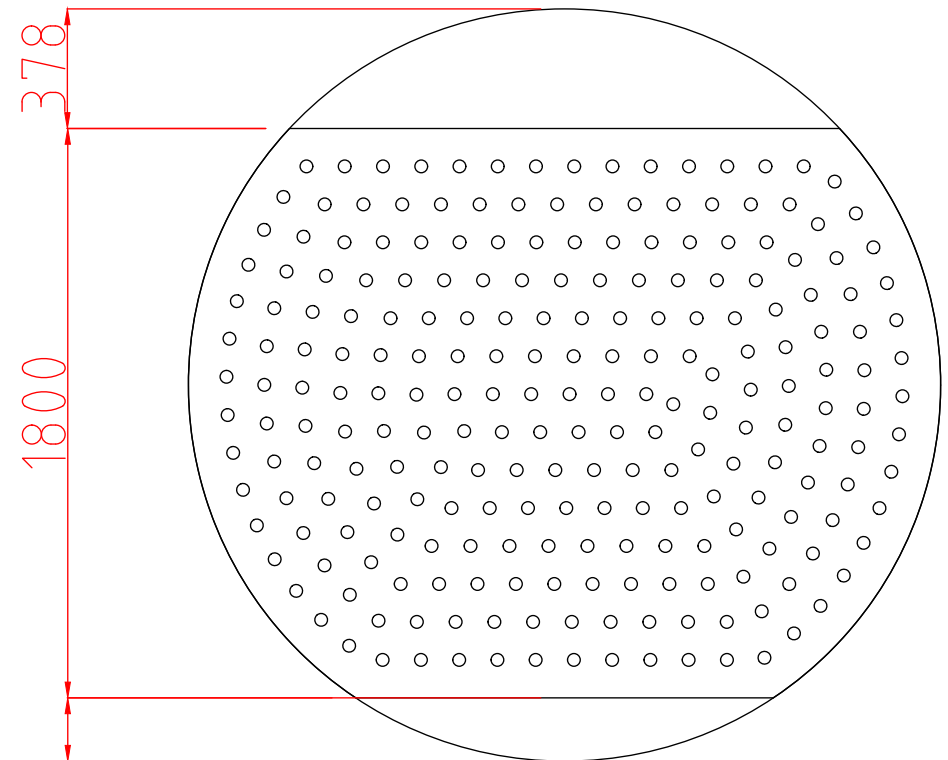

HOLES NO. = 132
SPACING = 12MM

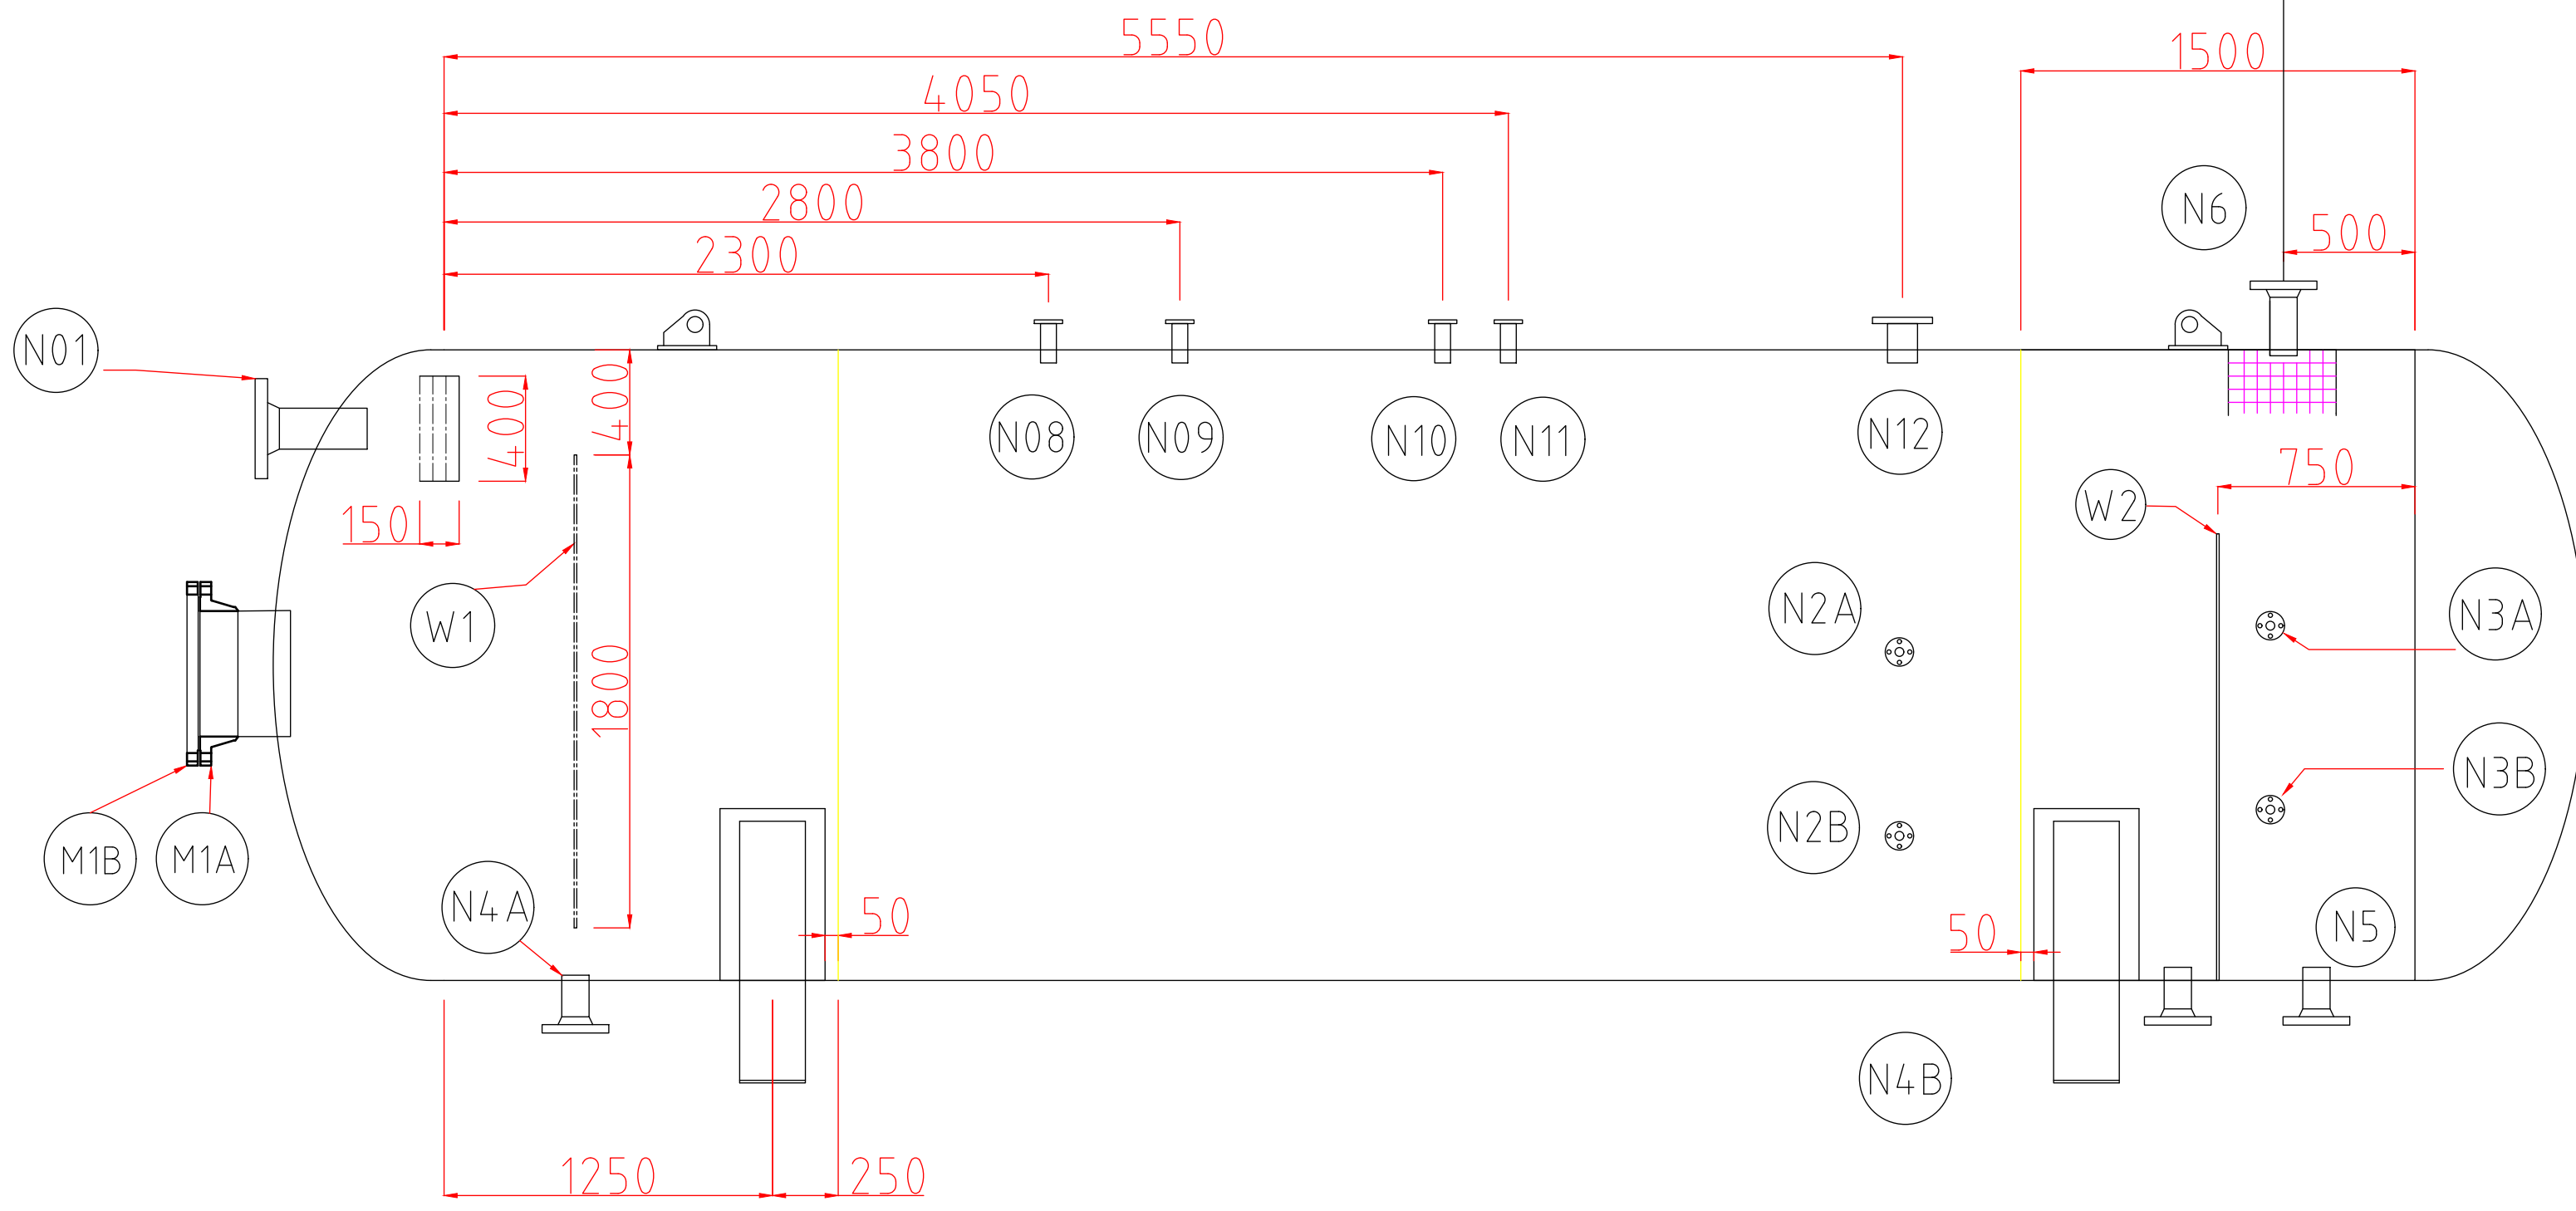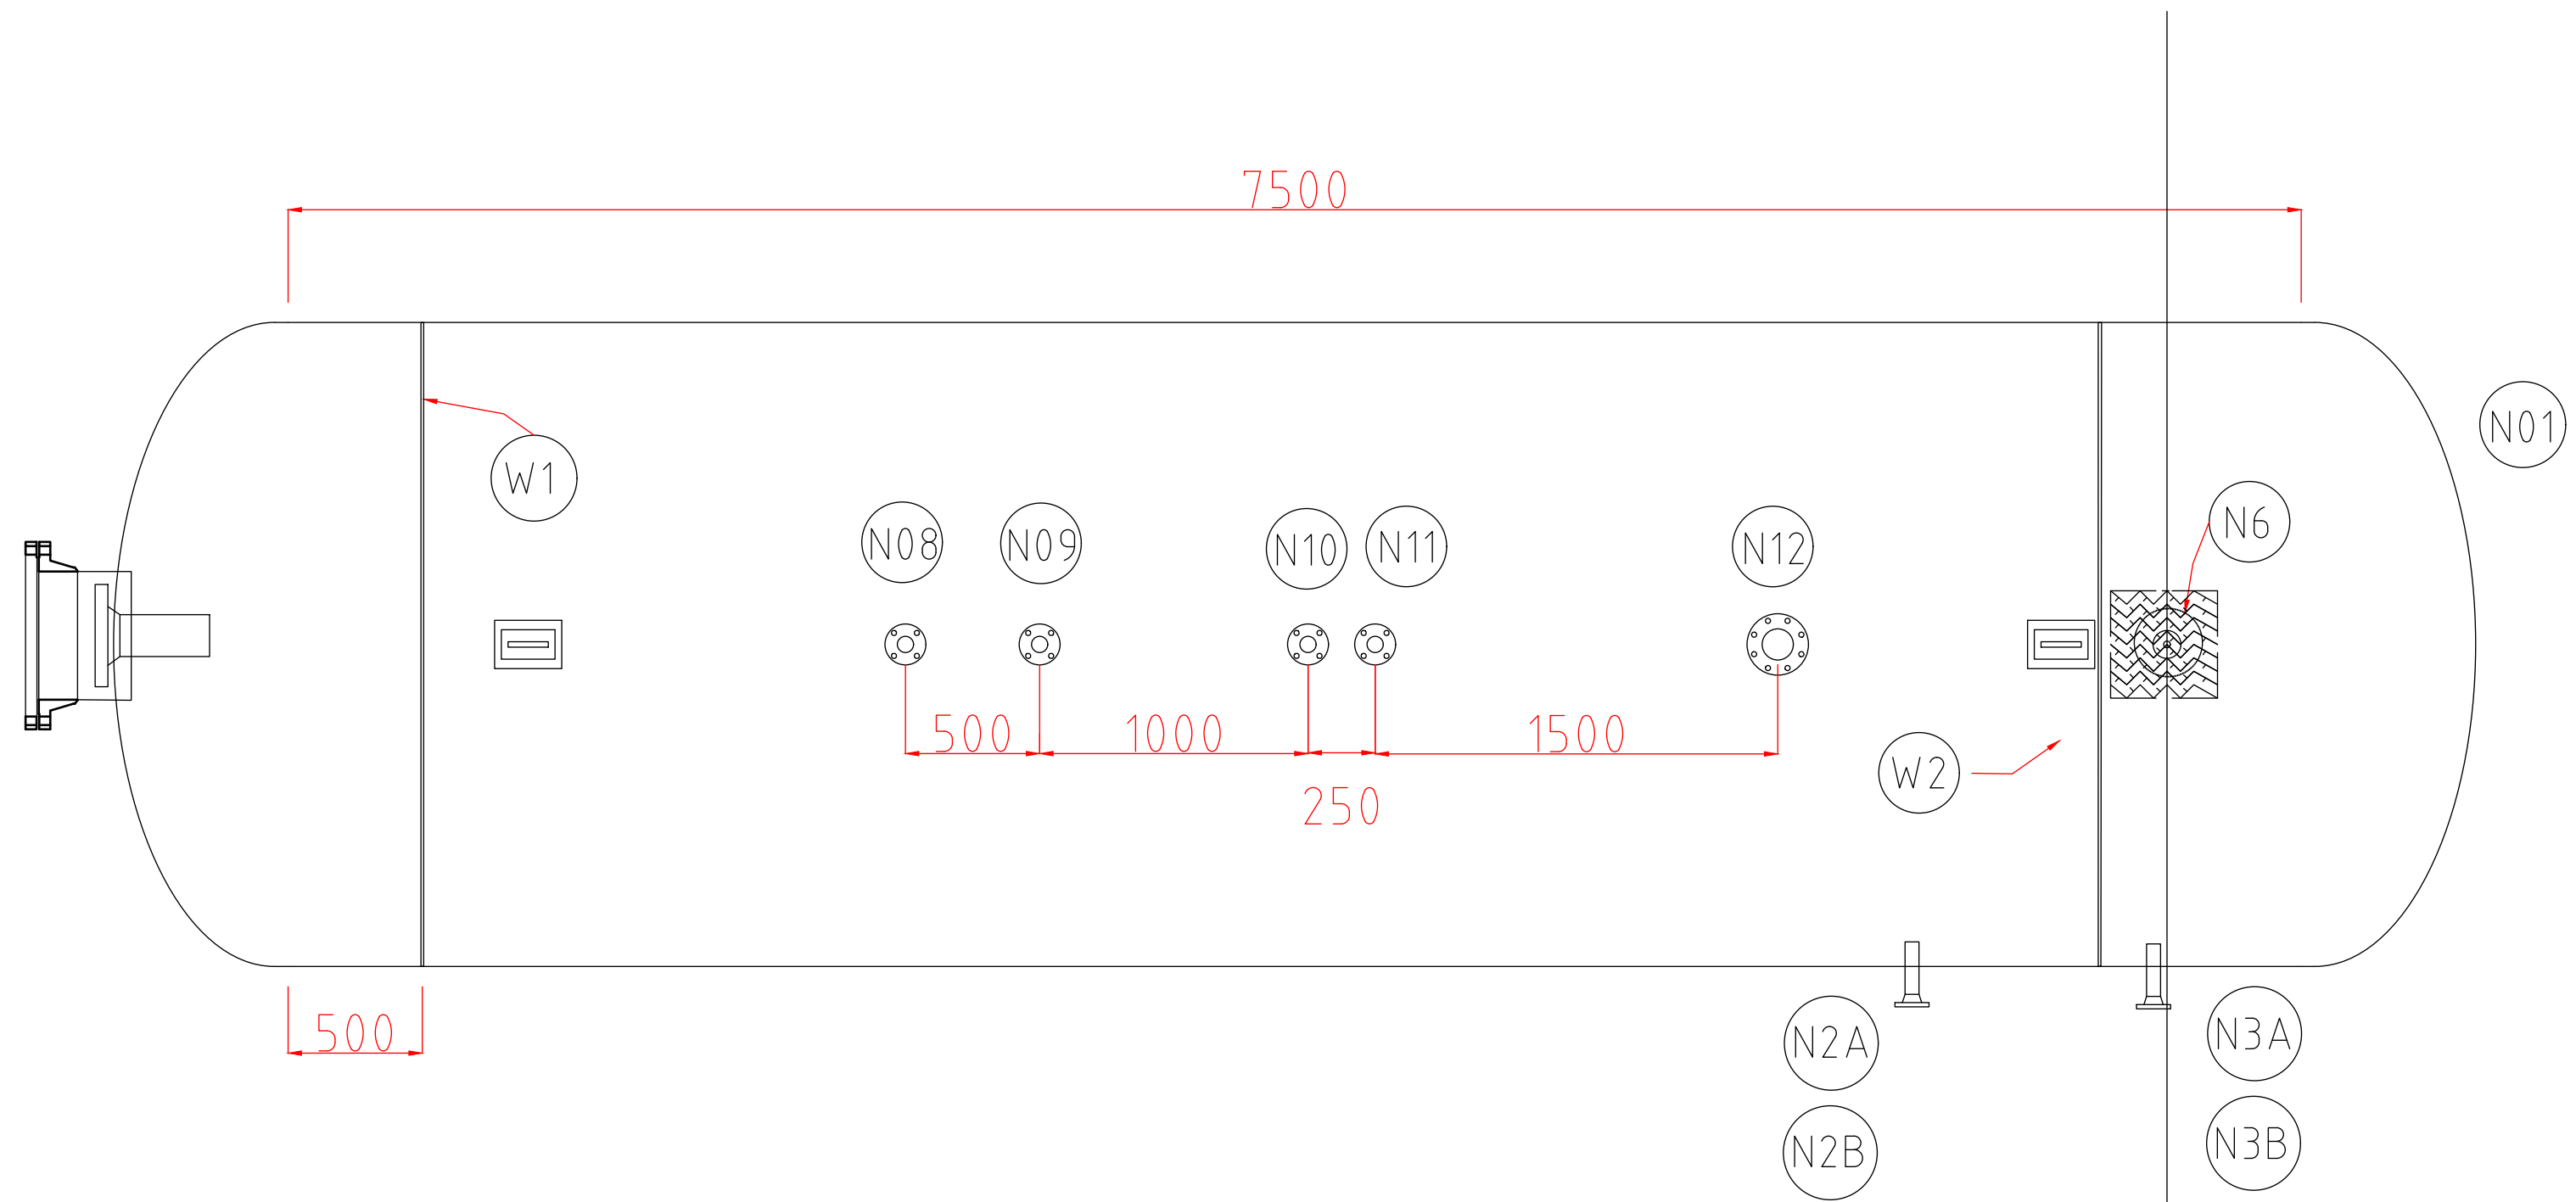

XSEC-ELEVATION A-A

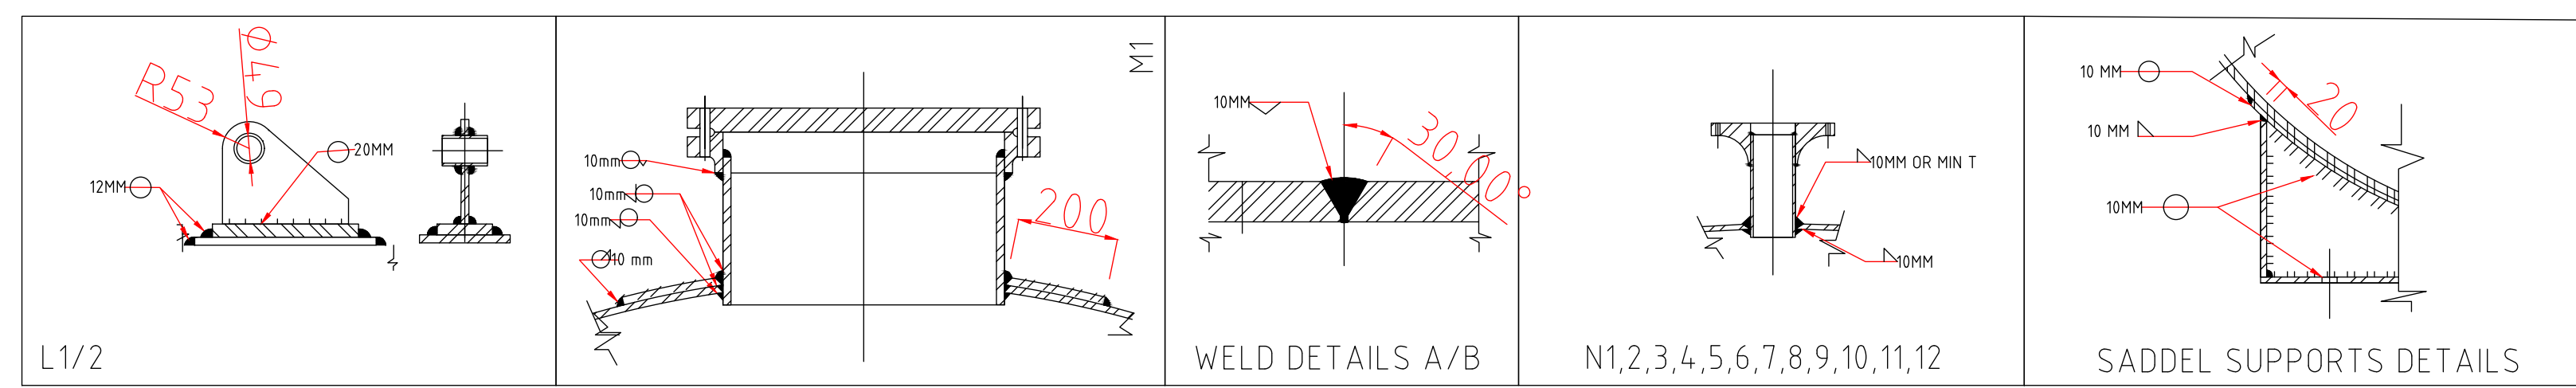

PROPERTY OF PETROTEC. REPRODUCTION OR UNAUTHORIZED USE WITHOUT PRIOR WRITTEN APPROVAL IS PROHIBED AND SUBJECT TO LEGAL ACTION.

NOZZLE	DIMS/ QTY	DESCRIPTION	SPECIFICATION
N1	6" 1	CRUDE OIL INLET NECK SMLS PIPE SCH 80-FLANGE: SO/RF #150-B16.5	SA106-GR.B SA105-B16.5
N2, A/B	2" 2	WATER/OIL LI/LC SIGHT GLASS/BRIDDLER NECK SMLS PIPE SCH 80-FLANGE: SO/RF #150-B16.5	SA106-GR.B SA105-B16.5
N3, A/B	2" 2	OIL/GAS LI/LC SIGHT GLASS/BRIDDLER NECK SMLS PIPE SCH 80-FLANGE: SO/RF #150-B16.5	SA106-GR.B SA105-B16.5
N4, A/B	4" 3	WATER OUTLET NECK SMLS PIPE SCH 80-FLANGE: SO/RF #150-B16.5	SA106-GR.B SA105-B16.5
N5	4" 1	OIL OUTLET NECK SMLS PIPE SCH 80-FLANGE: SO/RF #150-B16.5	SA106-GR.B SA105-B16.5
N6	4" 1	GAS OUTLET NECK SMLS PIPE SCH 80-FLANGE: SO/RF #150-B16.5	SA106-GR.B SA105-B16.5
N7	6" 1	INSPECTION NOZZLE NECK SMLS PIPE SCH 80-FLANGE: SO/RF #150-B16.5	SA106-GR.B SA105-B16.5
N8	2" 1	INJECTION INLET NECK SMLS PIPE SCH 80-FLANGE: SO/RF #150-B16.5	SA106-GR.B SA105-B16.5
N9	2" 1	INJECTION INLET NECK SMLS PIPE SCH 80-FLANGE: SO/RF #150-B16.5	SA106-GR.B SA105-B16.5
N10	2" 1	TI THERMOWELL NECK SMLS PIPE SCH 80-FLANGE: WN/RF #150-B16.5	SA106-GR.B SA105-B16.5
N11	2" 1	PI WELL NECK SMLS PIPE SCH 160-FLANGE: WN/RF #300-B16.5	SA106-GR.B SA105-B16.5
N12	4" 1	PSAFETY RELEIF VALVES NECK SMLS PIPE SCH 80-FLANGE: SO/RF #150-B16.5	SA106-GR.B SA105-B16.5
M1A	20" 1	MANHOLE -ROLLED PLATE 10 MM FLANGE SO/RF#150-B16.5	SA516-GR.70 -SA105-B16.5
M1B	20" 1	MANHOLE BLIND FLANGE#150 B16.5 WITH DAVIS ARM AND SUPPORTING HING	SA105
H 1/2	- 1	ELLIPTICAL HEADS PLATES 1 & 2 10 MM X1900 X 475 MMX100 MM ST. FLANGE	SA516-GR.70 COLD FORMING
W1	- 2	DEFLECTOR PLATE INTERNAL	SA516-GR.70
W2	- 1	WEIR PLATE INTERNALS	SA516-GR.70
L	- 2	LIFTING LUGS 20 MM X 150 MM X Ø 50.8 MM HOLE	SA283-GR.C

APPROVED FOR CONSTRUCTION

DATE:
04-05-2026

PETROTEC

INDUSTRIAL ENGINEERING COMPANY

3-PHASE SEPARATOR

GENERAL ASEMBLY - MECHANICAL DETAILS V-101

DWG. NO.	DRAWN BY	DESIGNED BY	DATE
PT-413-01	ENG. I.H	ENG. TAREK HAMMAD	5/4/2026