



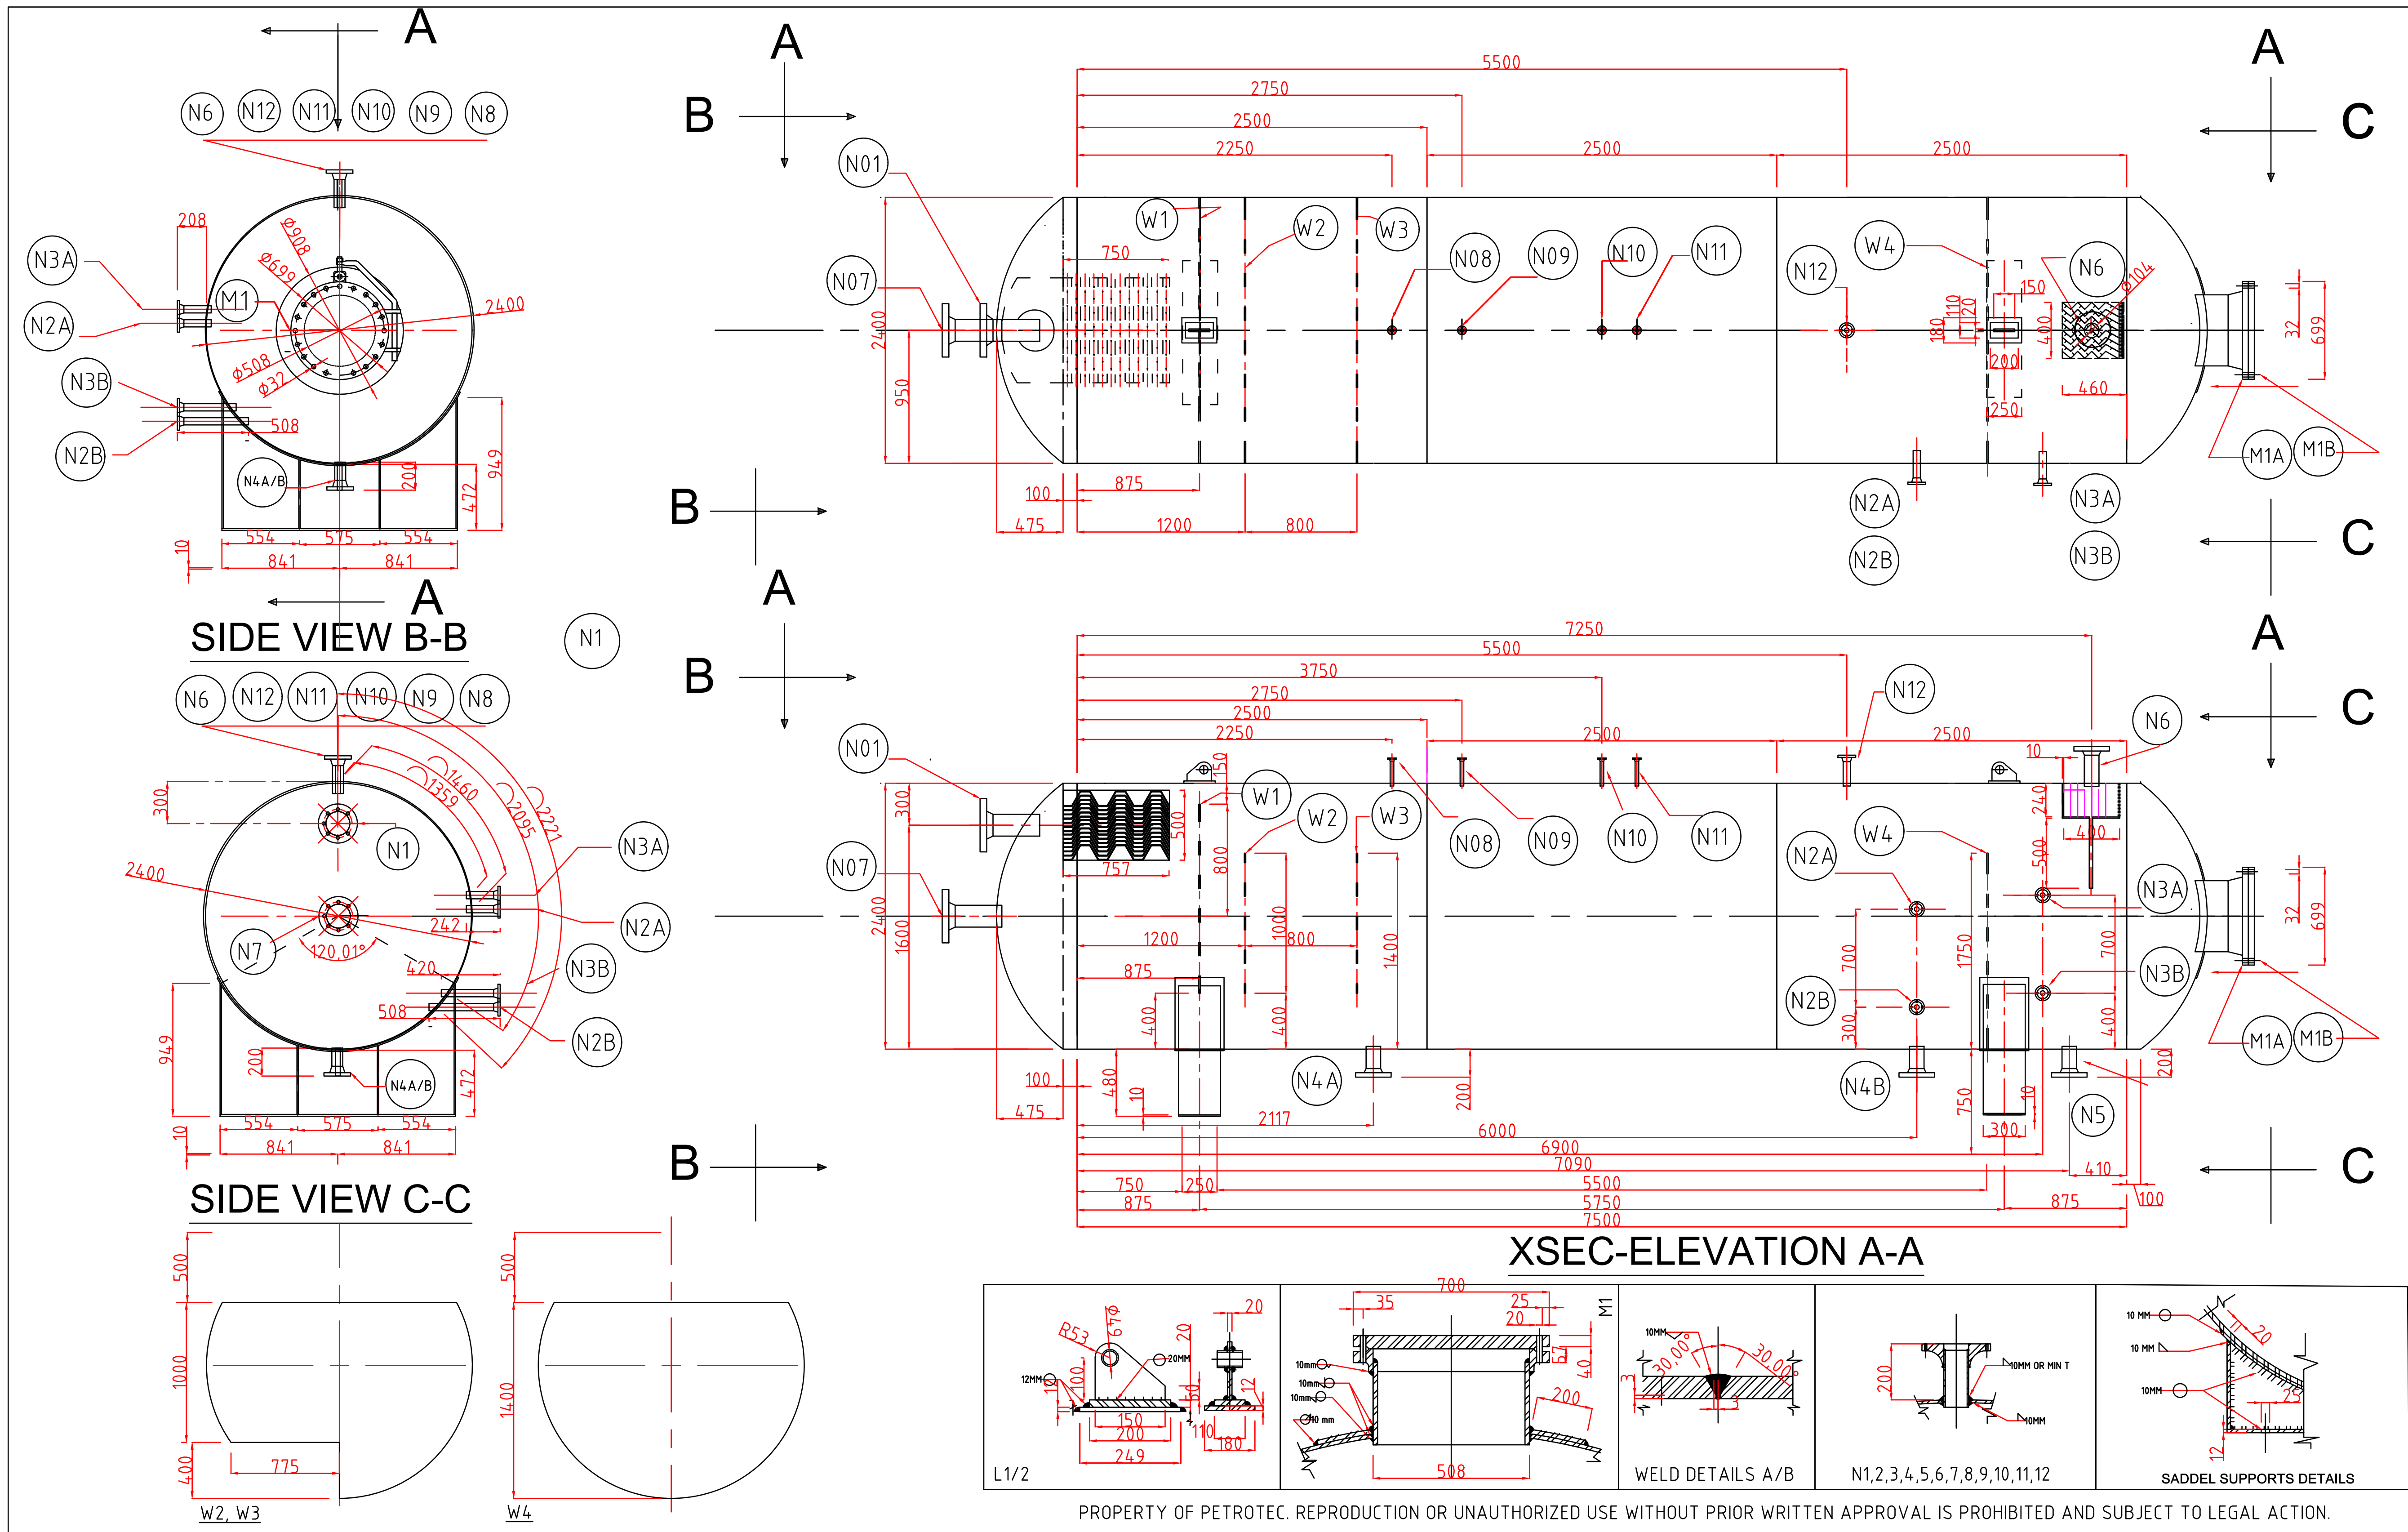

V-101				
LP PRODUCTION SEPARATOR				
SIZE (ODXL): 2.4M X 7.5M				
D.P/D.T: 60 PSIG / 0 TO 100°C				
D/OP CAPACITY: 20000/±10000 BPD				
NOZZLE	DIMS	QTY	DESCRIPTION	SPECIFICATION
N1	6"	1	CRUDE OIL INLET NECK SMLS PIPE SCH.80-FLANGE: SO/RF #150-B16.5	SA106-GR.B SA105-B16.5
N2, A/B	2"	2	WATER/OIL LI/LC SIGHT GLASS/BRIDLE NECK SMLS PIPE SCH.80-FLANGE: SO/RF #150-B16.5	SA106-GR.B SA105-B16.5
N3, A/B	2"	2	OIL/GAS LI/LC SIGHT GLASS/BRIDLE NECK SMLS PIPE SCH.80-FLANGE: SO/RF #150-B16.5	SA106-GR.B SA105-B16.5
N4, A/B	4"	3	WATER OUTLET NECK SMLS PIPE SCH.80-FLANGE: SO/RF #150-B16.5	SA106-GR.B SA105-B16.5
N5	4"	1	OIL OUTLET NECK SMLS PIPE SCH.80-FLANGE: SO/RF #150-B16.5	SA106-GR.B SA105-B16.5
N6	4"	1	GAS OUTLET NECK SMLS PIPE SCH.80-FLANGE: SO/RF #150-B16.5	SA106-GR.B SA105-B16.5
N7	6"	1	INSPECTION NOZZLE NECK SMLS PIPE SCH.80-FLANGE: SO/RF #150-B16.5	SA106-GR.B SA105-B16.5
N8	1"	1	INJECTION INLET NECK SMLS PIPE SCH.80-FLANGE: SO/RF #150-B16.5	SA106-GR.B SA105-B16.5
N9	1"	1	INJECTION INLET NECK SMLS PIPE SCH.80-FLANGE: SO/RF #150-B16.5	SA106-GR.B SA105-B16.5
N10	1"	1	TI THERMOWELL NECK SMLS PIPE SCH.80-FLANGE: WN/RF #150-B16.5	SA106-GR.B SA105-B16.5
N11	1"	1	PI WELL NECK SMLS PIPE SCH.160-FLANGE: WN/RF #300-B16.5	SA106-GR.B SA105-B16.5
N12	2"	1	PSAFETY RELIEF VALVES NECK SMLS PIPE SCH.80-FLANGE: SO/RF #150-B16.5	SA106-GR.B SA105-B16.5
M1A	20"	1	MANHOLE -ROLLED PLATE 10 MM FLANGE SO/RF#150-B16.5	SA516-GR.70 -SA105-B16.5
M1B	20"	1	MANHOLE BLIND FLANGE#150 B16.5 WITH DAVIS ARM AND SUPPORTING HING	SA105
M1C	20"	1	MANHOLE NOZZLE REINFORCEMENT PLATE WIDTH 200 MM X 10 MM THK	SA516-GR.70
M1D	20"	1	MANHOLE DAVIS ARM SOLID BAR 1.5" SUPPORTING HING PLATE 20MM THK	SA36- SA283-GR.C
S1,2,3	-	1	SHELL PLATES TEIR 1 10 MM X 2500 MM X 6000 MM	SA516-GR.70
H 1/2	-	1	ELLIPTICAL HEADS PLATES 1 & 2 10 MM X1900 X 475 MMX100 MM ST. FLANGE	SA516-GR.70 COLD FORMING
W1	-	1	DEFLECTOR PLATE INTERNAL W1 1350 MM HEIGHT t= 10 mm Defuser Plates QTY 14 x 6 mm thk corrugated	SA516-GR.70
W2,3,4	-	3	WEIR PLATES INTERNALS QTY 3 1400 MM HEIGHT t=10 mm	SA516-GR.70
L	-	2	LIFTING LUGS 20 MM X 150 MM X Ø 50.8 MM HOLE	SA283-GR.C
APPROVED FOR CONSTRUCTION				DATE: 04-05-2026
PETROTEC				
INDUSTRIAL ENGINEERING COMPANY				
3-PHASE SEPARATOR				
GENERAL ASSEMBLY – MECHANICAL DETAILS V-101				
DWG. NO.	DRAWN BY	DESIGNED BY		DATE
PT-413-01	ENG. I.H	ENG. TAREK HAMMAD		04-May-26

PROPERTY OF PETROTEC. REPRODUCTION OR UNAUTHORIZED USE WITHOUT PRIOR WRITTEN APPROVAL IS PROHIBITED AND SUBJECT TO LEGAL ACTION.

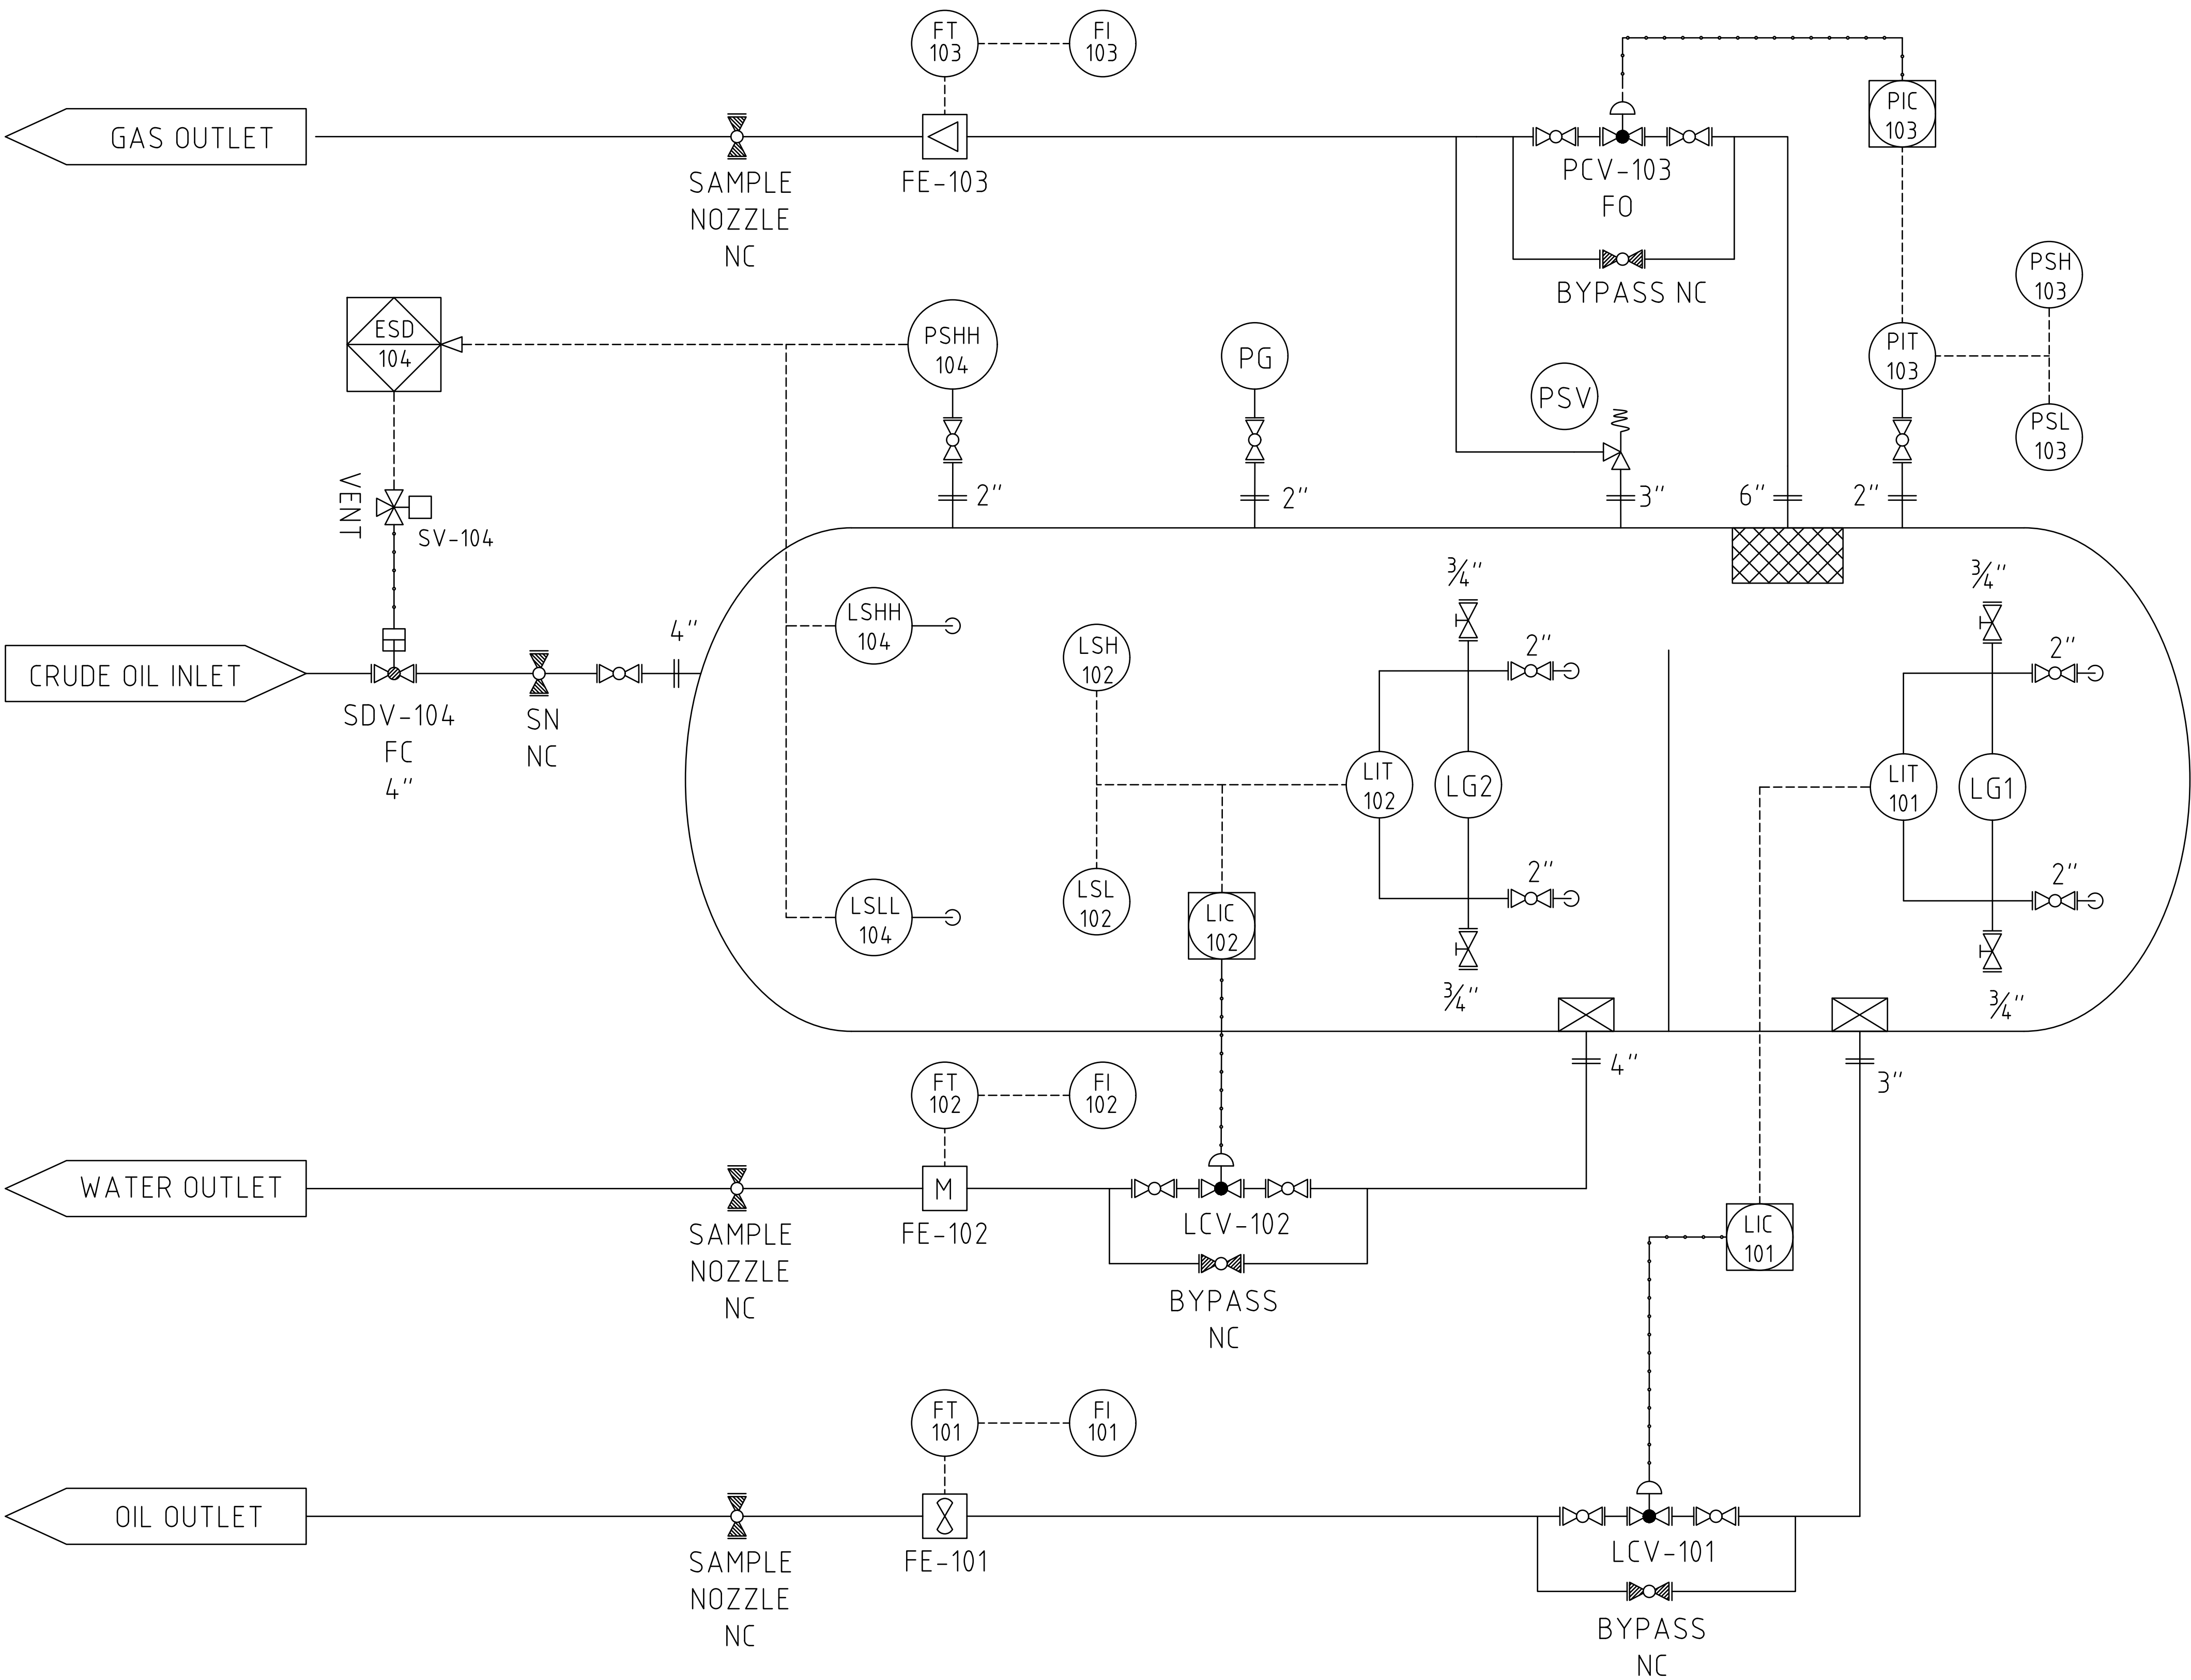

V-101

LP - PRODUCTION SEPARATOR
2.4M OD × 7.5M LENGTH
D/OP PRESSURE: 60/ - PSIG
D/OP CAPACITY: 20000/±10000 BPD

LINE SYMBOLS

PROCESS LINE
SIGNAL LINE
AIR LINE

FLOW METER ELEMENT

TURBINE
VORTEX
MAGNETIC

VALVES

BALL (SHUTDOWN)
GLOBE (CONTROL)
GAUGE COCK

PROCESS ALARMS

PSH-103 — High pressure alarm.
PSL-103 — Low pressure alarm.
LSH-102 — High liquid level alarm.
LSL-102 — Low liquid level alarm.

SHUTDOWN TRIPS

PSHH-104 — PRESSURE SWITCH HIGH HIGH.
LSHH-104 — LEVEL SWITCH HIGH HIGH
LSLL-104 — LEVEL SWITCH LOW LOW

PETROTEC

INDUSTRIAL ENGINEERING COMPANY

DRAWING TITLE

PIPING AND INSTRUMENTATION DIAGRAM
P&ID FOR LP PRODUCTION SEPARATOR V-101

DWG. NO.	DRAWN BY	DESIGNED BY	DATE
PT-413-03	ENG. I.H	ENG. TAREK HAMMAD	30-May-26