


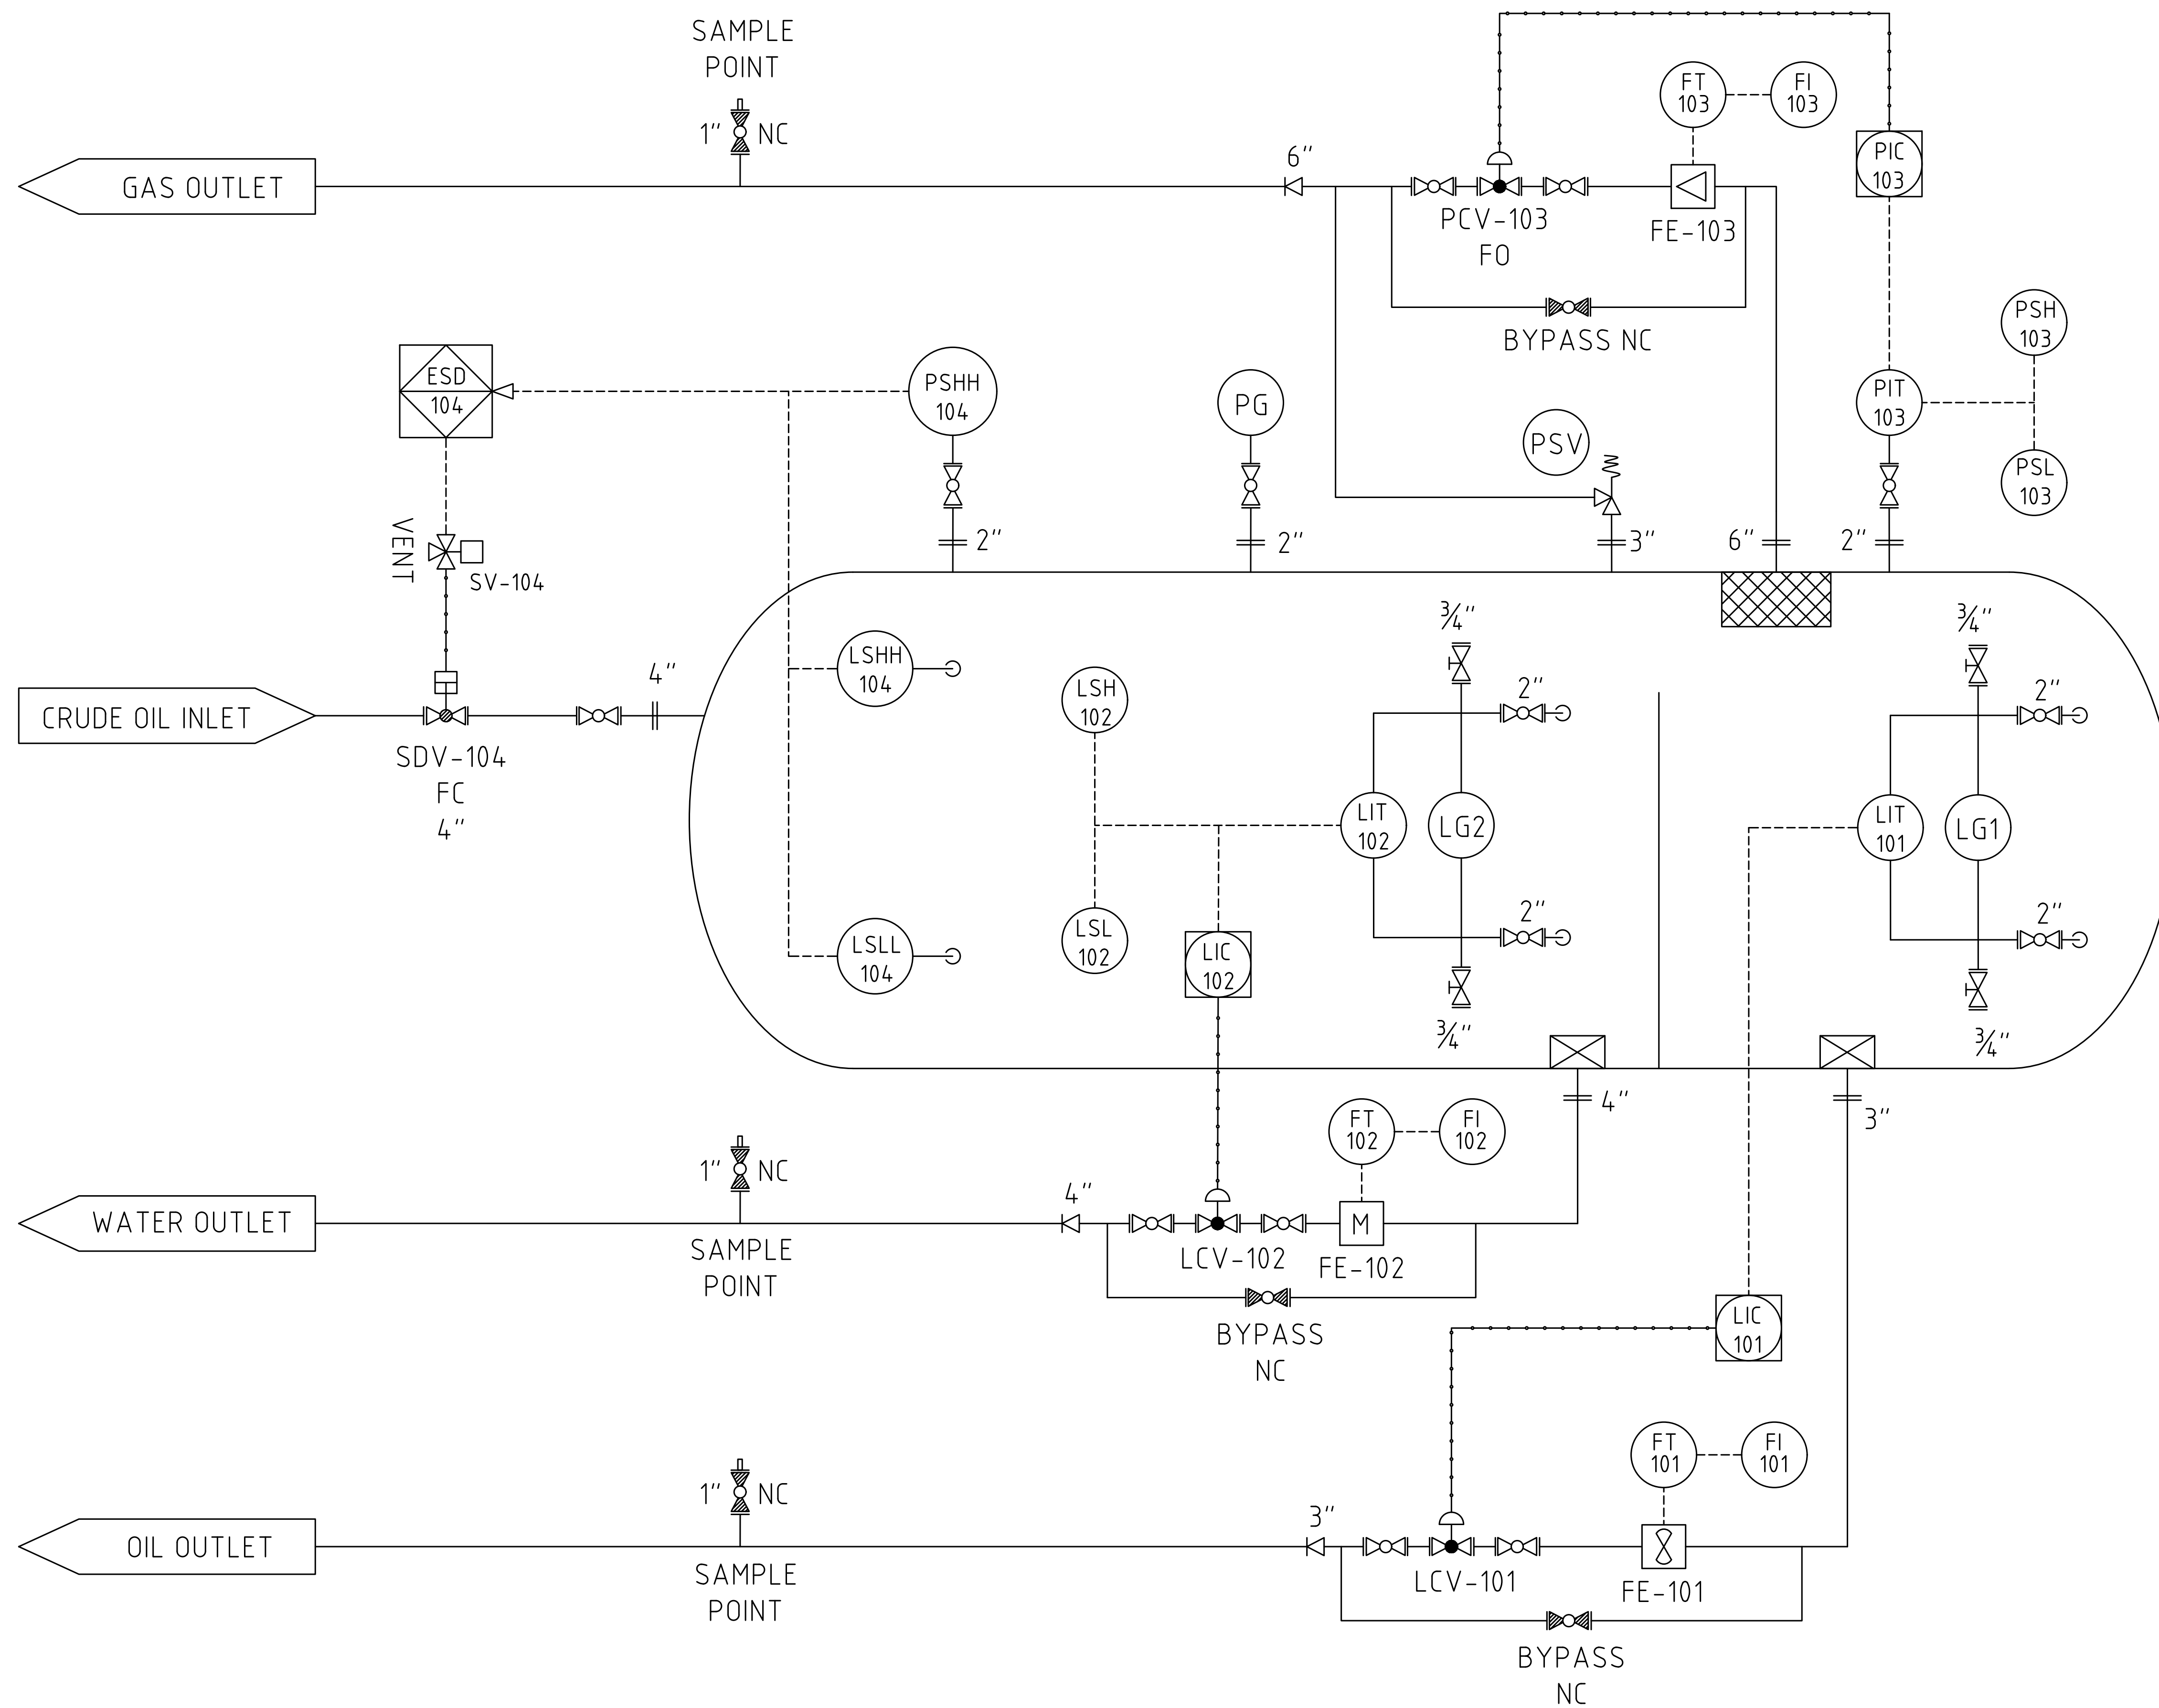

V-101

LP - PRODUCTION SEPARATOR  
2.4M OD × 7.5M LENGTH  
D/OP PRESSURE: 60/- PSIG  
D/OP CAPACITY: 20000/±10000 BPD

#### LINE SYMBOLS

PROCESS LINE  
SIGNAL LINE  
AIR LINE

#### FLOW METER ELEMENT

TURBINE  
VORTEX  
MAGNETIC

#### VALVES

BALL (SHUTDOWN)  
GLOBE (CONTROL)  
GAUGE COCK

#### PROCESS ALARMS

PSH-103 — High pressure alarm.  
PSL-103 — Low pressure alarm.  
LSH-102 — High liquid level alarm.  
LSL-102 — Low liquid level alarm.

#### SHUTDOWN TRIPS

PSHH-104 — PRESSURE SWITCH HIGH HIGH.  
LSHH-104 — LEVEL SWITCH HIGH HIGH  
LSLL-104 — LEVEL SWITCH LOW LOW

**PETROTEC**

INDUSTRIAL ENGINEERING COMPANY

#### DRAWING TITLE

PIPING AND INSTRUMENTATION DIAGRAM  
P&ID FOR LP PRODUCTION SEPARATOR V-101

DWG. NO.

DRAWN BY

DESIGNED BY

DATE

PT-413-03

ENG. I.H

ENG. TAREK  
HAMMAD

30-May-26

PROPERTY OF PETROTEC. REPRODUCTION OR UNAUTHORIZED USE WITHOUT  
PRIOR WRITTEN APPROVAL IS PROHIBITED AND SUBJECT TO LEGAL ACTION.