


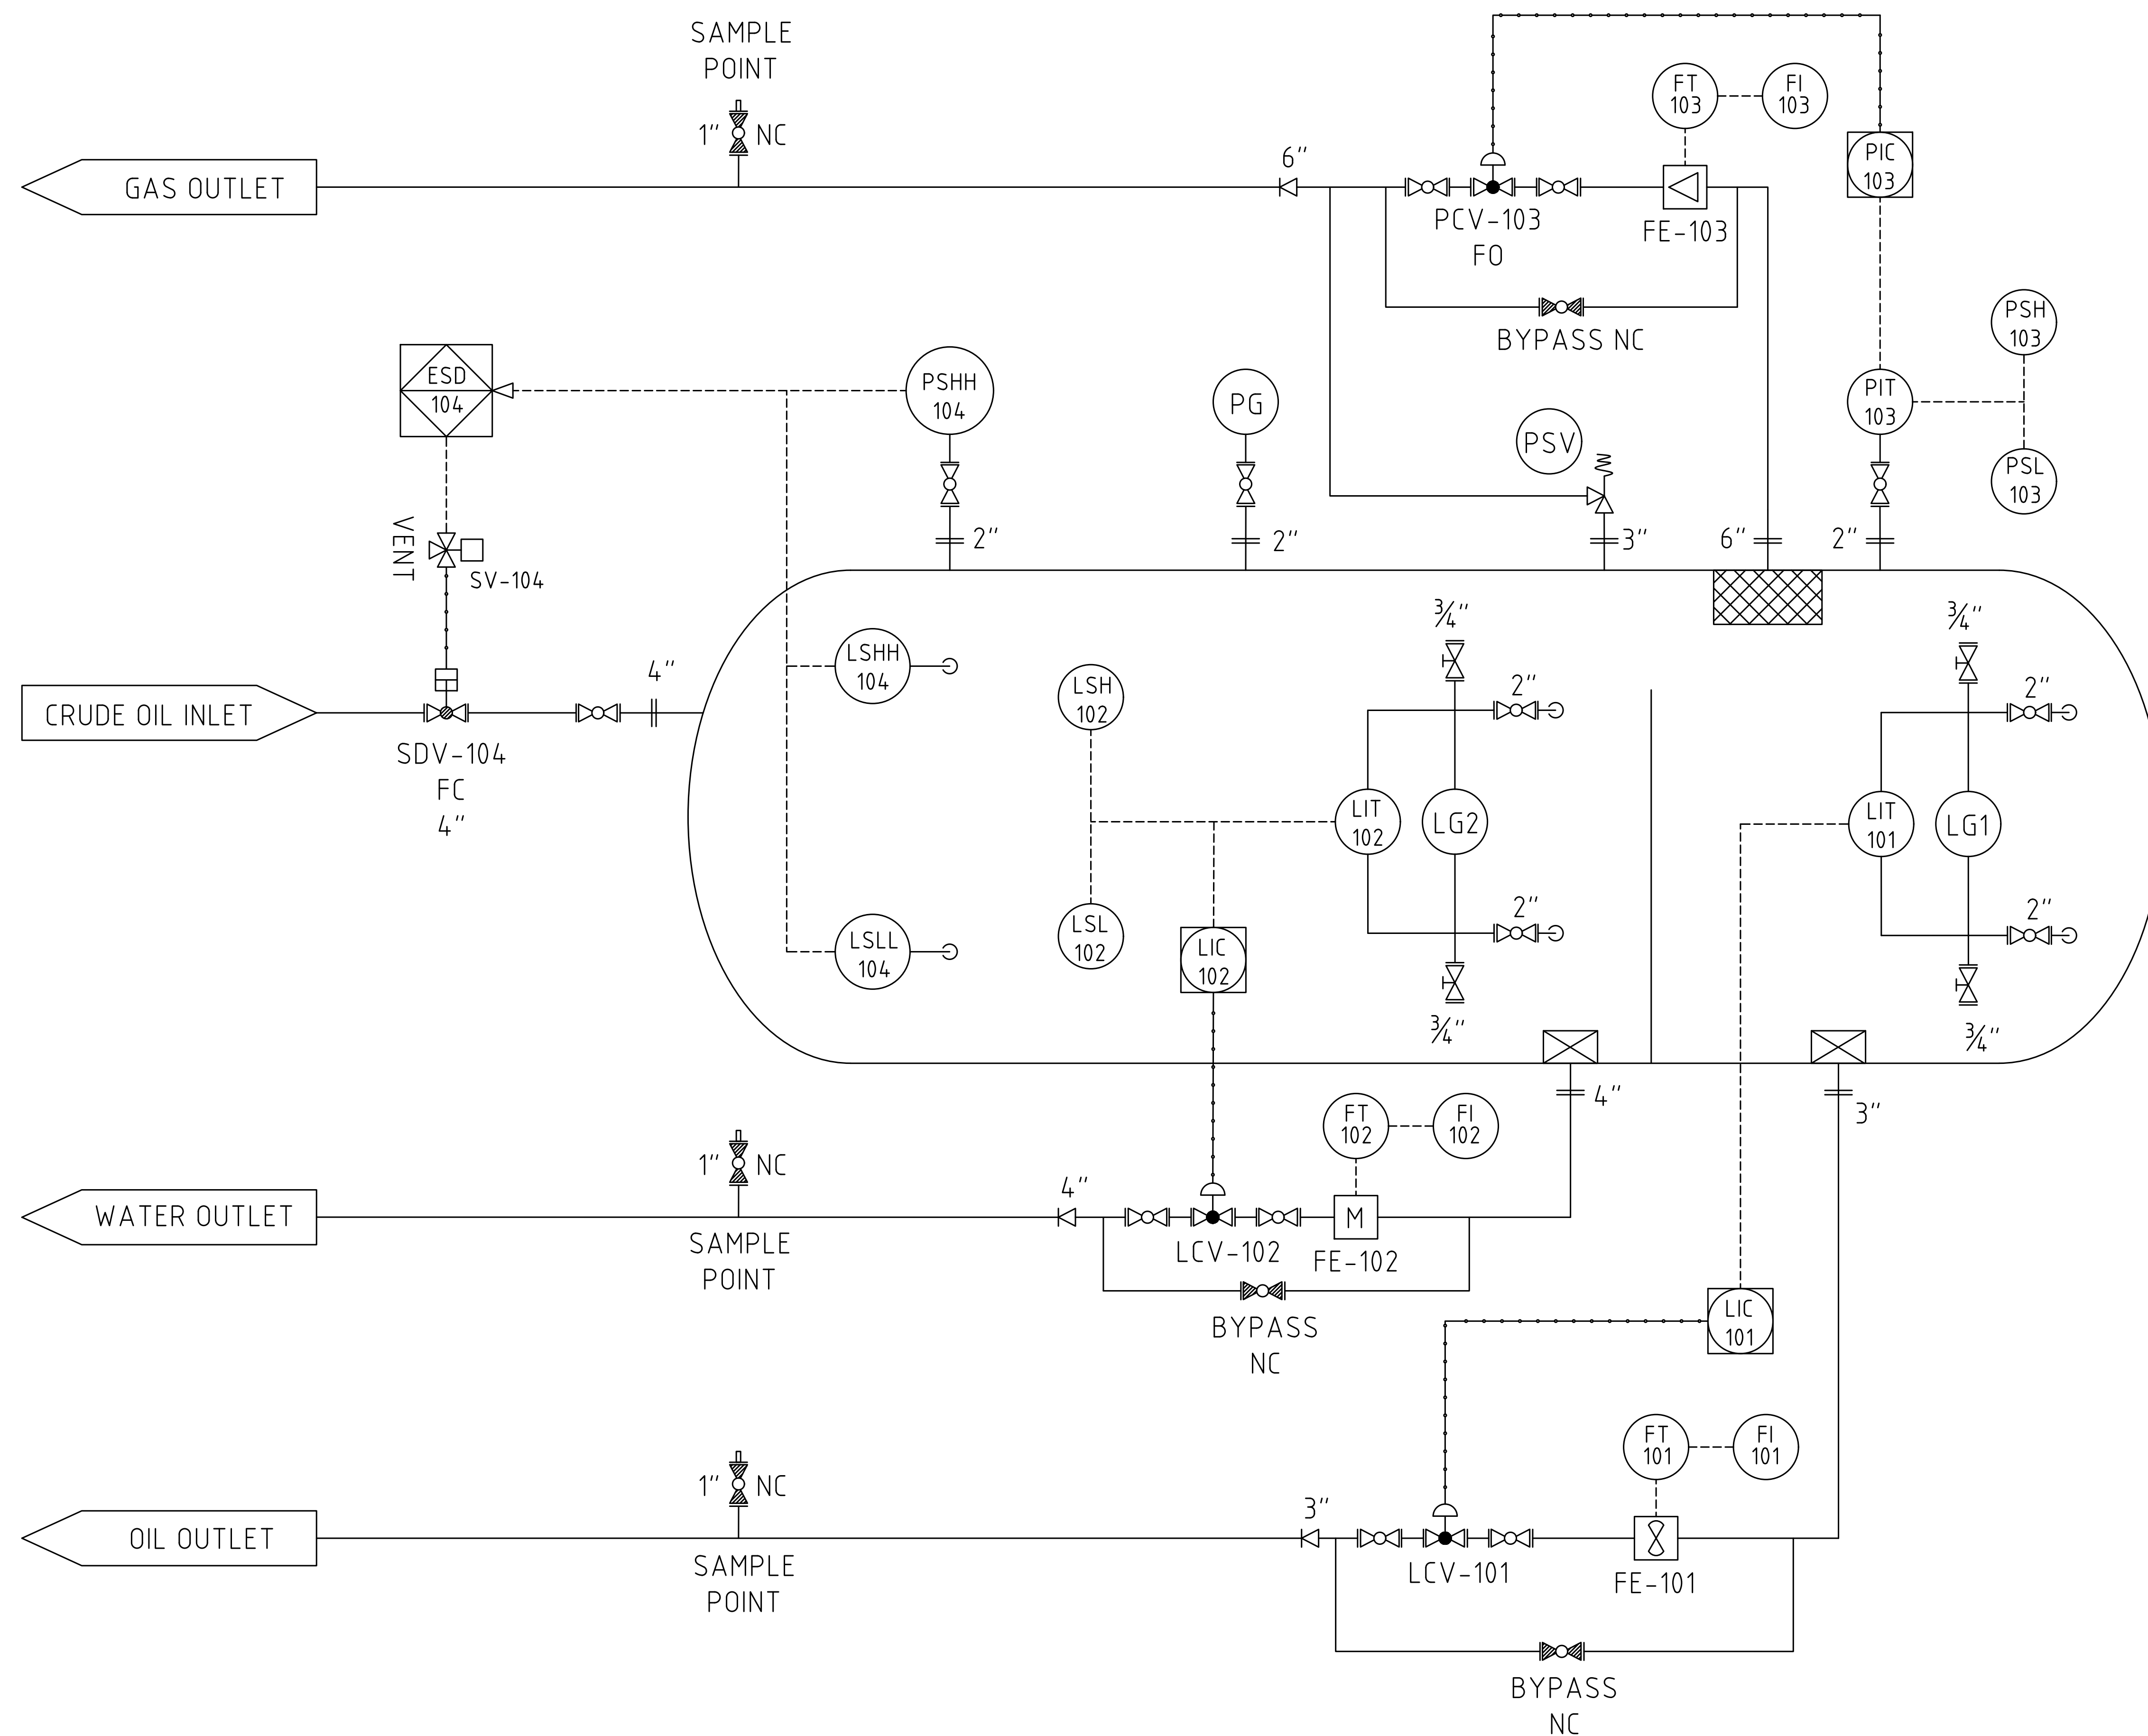

V-101

LP - PRODUCTION SEPARATOR
2.4M OD × 7.5M LENGTH
D/OP PRESSURE: 60/- PSIG
D/OP CAPACITY: 20000/±10000 BPD

LINE SYMBOLS

PROCESS LINE
SIGNAL LINE
AIR LINE

FLOW METER ELEMENT

TURBINE
VORTEX
MAGNETIC

VALVES

BALL (SHUTDOWN)
GLOBE (CONTROL)
GAUGE COCK

PROCESS ALARMS

PSH-103 — High pressure alarm.
PSL-103 — Low pressure alarm.
LSH-102 — High liquid level alarm.
LSL-102 — Low liquid level alarm.

SHUTDOWN TRIPS

PSHH-104 — PRESSURE SWITCH HIGH HIGH.
LSHH-104 — LEVEL SWITCH HIGH HIGH
LSLL-104 — LEVEL SWITCH LOW LOW

PETROTEC

INDUSTRIAL ENGINEERING COMPANY

DRAWING TITLE

PIPING AND INSTRUMENTATION DIAGRAM
P&ID FOR LP PRODUCTION SEPARATOR V-101

DWG. NO.	DRAWN BY	DESIGNED BY	DATE
PT-413-03	ENG. I.H	ENG. TAREK HAMMAD	30-May-26

PROPERTY OF PETROTEC. REPRODUCTION OR UNAUTHORIZED USE WITHOUT
PRIOR WRITTEN APPROVAL IS PROHIBITED AND SUBJECT TO LEGAL ACTION.