


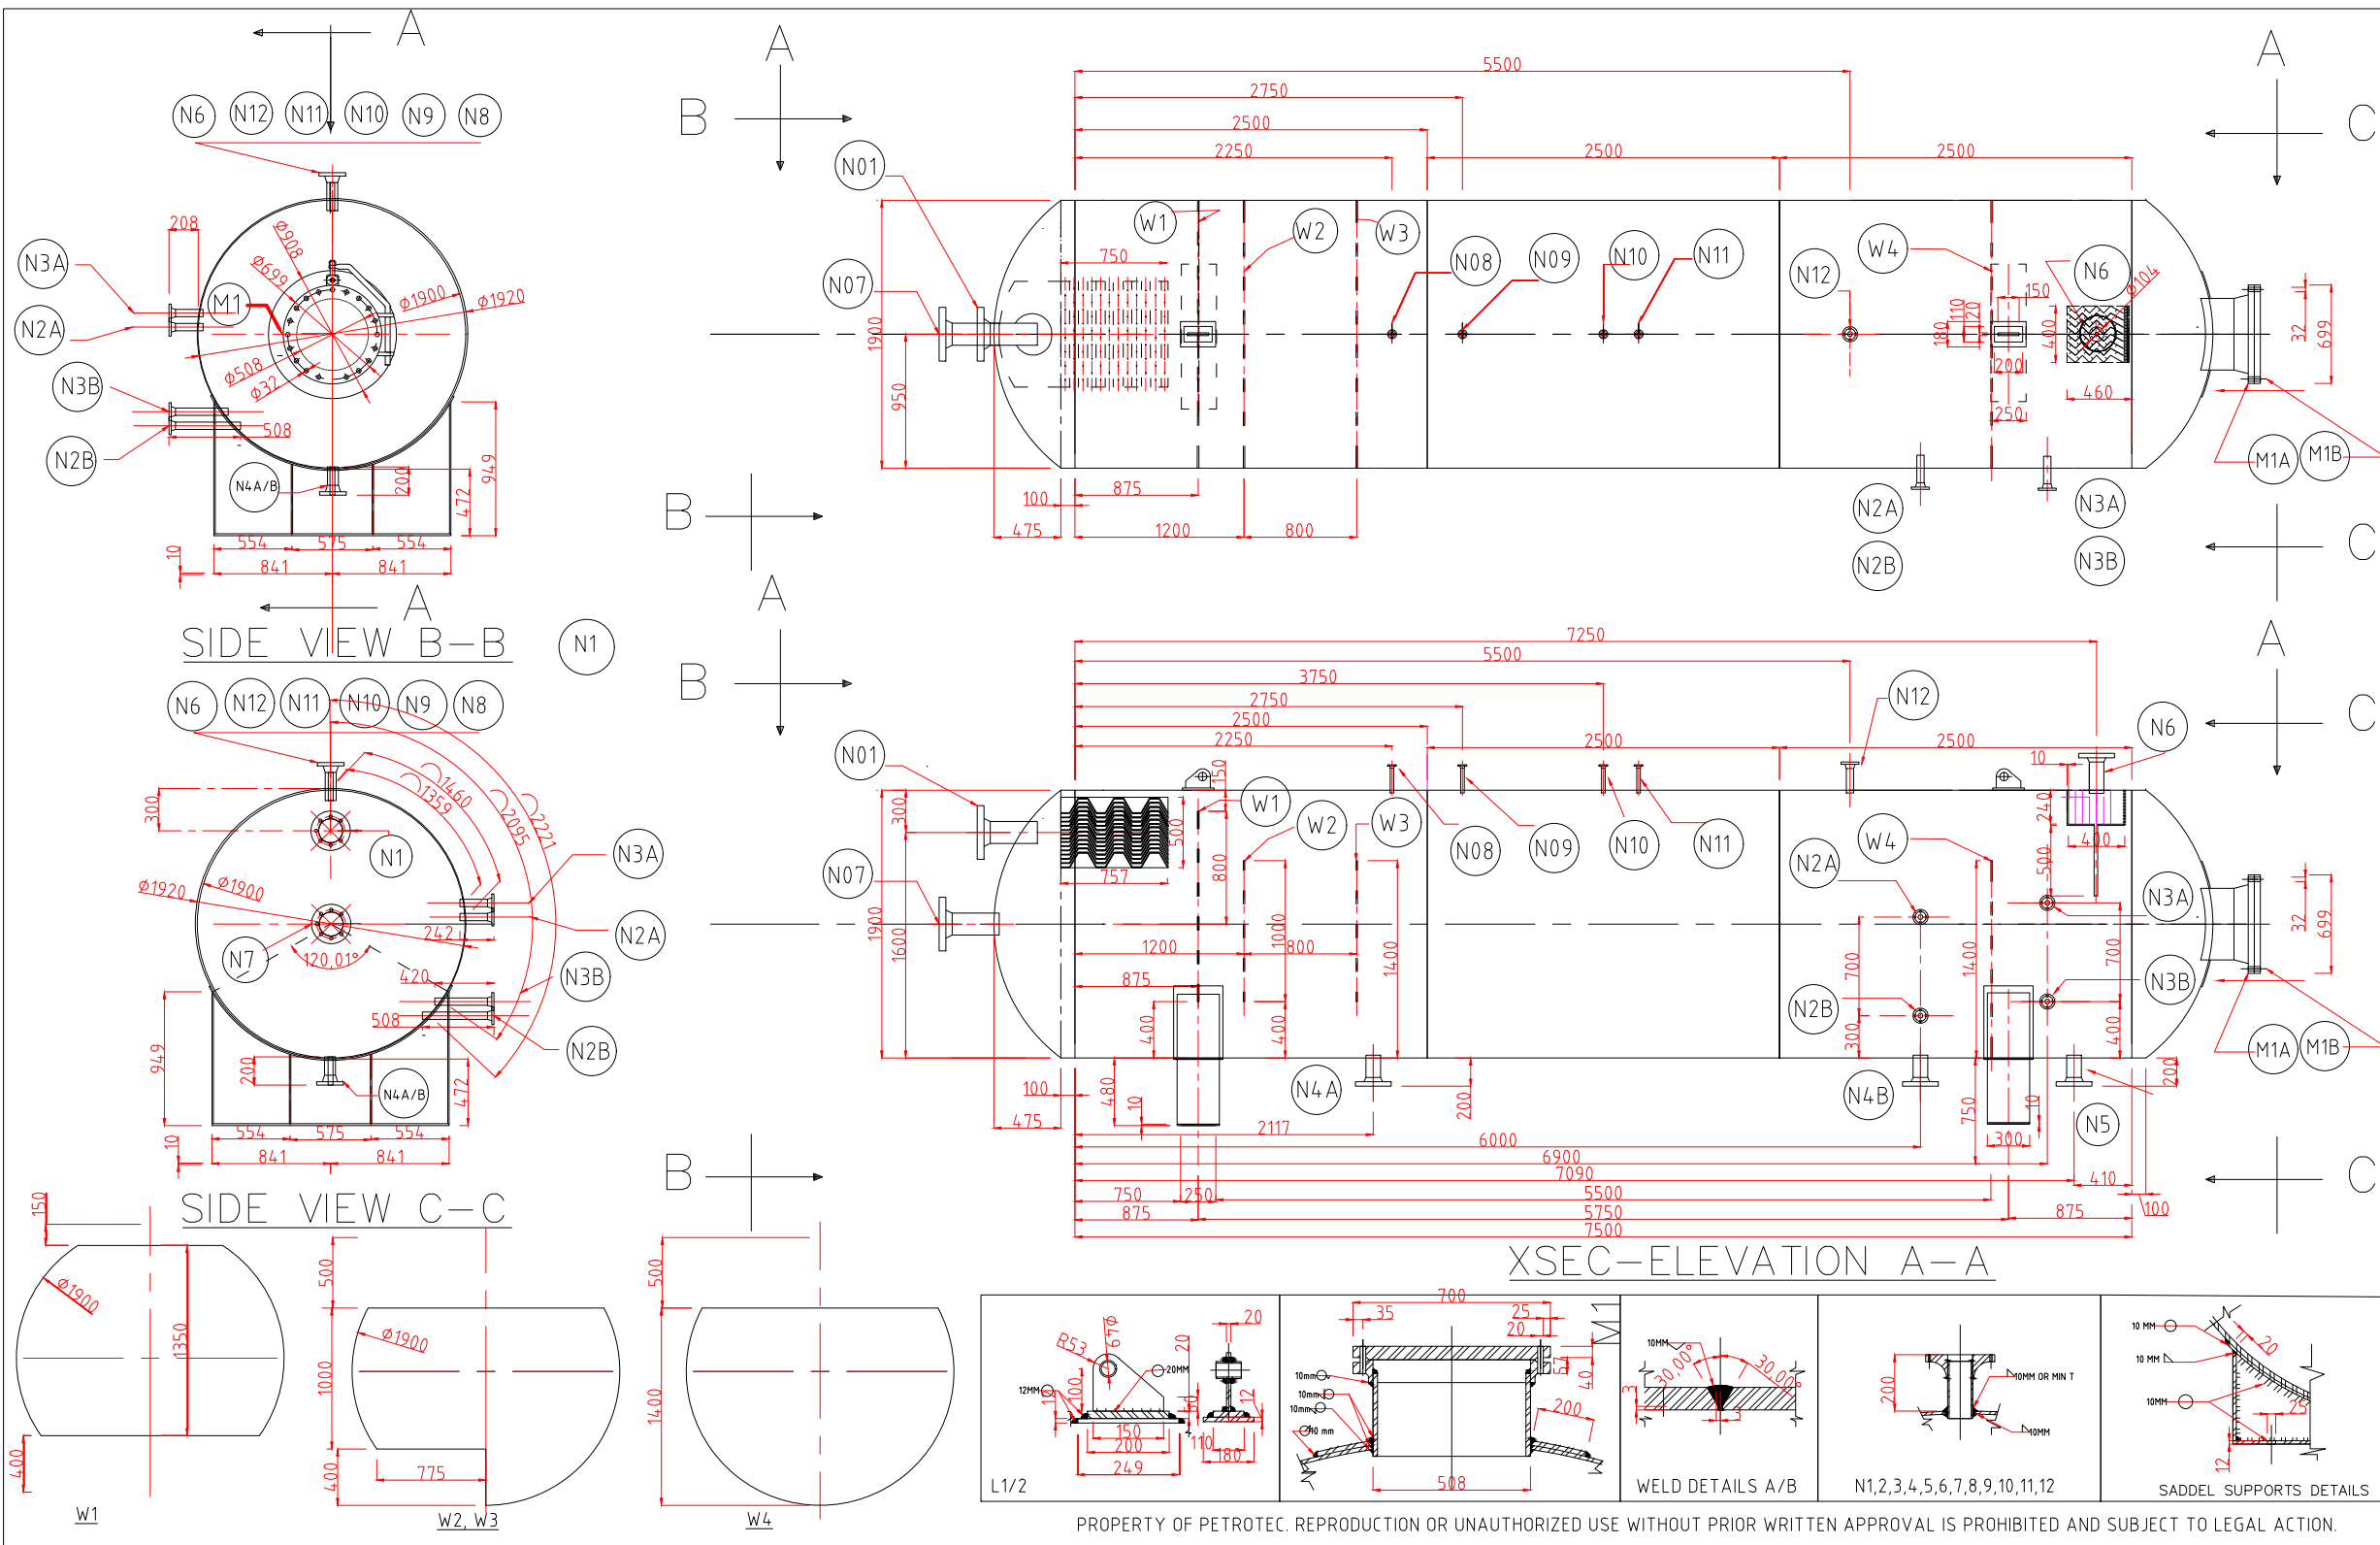

- GENERAL NOTES :
- CODE OF CONSTRUCTION - ASME SEC.VIII-DIV.I-EDD 2017 - STAMPED.
 - MAWP: For Shell side=75 psig
 - MDMT=+ 30 F
 - Hydrotest: Shell side=1.3x75=97.5 psig for duration of 1/2 hour.
 - UW-2 FOR LETHAL SERVICE - NON LETHAL.
 - IMPACT TEST Exempted - UG - 22 (F) , UCS.
 - Stress Relief exempted as per ASME STD.
 - Dimension Tolerance as per ASME SEC VIII.
 - E= 0.60 in Calculation as per ASME STD conditions.

NOZZLE	DIMS	QTY	DESCRIPTION	SPECIFICATION
N1	6"	1	CRUDE OIL INLET NECK SMLS PIPE SCH.80-FLANGE: SO/RF #150-B16.5	SA106-GR.B SA105-B16.5
N2, A/B	2"	2	WATER/OIL LI/LC SIGHT GLASS/BRIDLE NECK SMLS PIPE SCH.80-FLANGE: SO/RF #150-B16.5	SA106-GR.B SA105-B16.5
N3, A/B	2"	2	OIL/GAS LI/LC SIGHT GLASS/BRIDLE NECK SMLS PIPE SCH.80-FLANGE: SO/RF #150-B16.5	SA106-GR.B SA105-B16.5
N4, A/B	4"	3	WATER OUTLET NECK SMLS PIPE SCH.80-FLANGE: SO/RF #150-B16.5	SA106-GR.B SA105-B16.5
N5	4"	1	OIL OUTLET NECK SMLS PIPE SCH.80-FLANGE: SO/RF #150-B16.5	SA106-GR.B SA105-B16.5
N6	4"	1	GAS OUTLET NECK SMLS PIPE SCH.80-FLANGE: SO/RF #150-B16.5	SA106-GR.B SA105-B16.5
N7	6"	1	INSPECTION NOZZLE NECK SMLS PIPE SCH.80-FLANGE: SO/RF #150-B16.5	SA106-GR.B SA105-B16.5
N8	1"	1	INJECTION INLET NECK SMLS PIPE SCH.80-FLANGE: SO/RF #150-B16.5	SA106-GR.B SA105-B16.5
N9	1"	1	INJECTION INLET NECK SMLS PIPE SCH.80-FLANGE: SO/RF #150-B16.5	SA106-GR.B SA105-B16.5
N10	1"	1	TI THERMOWELL NECK SMLS PIPE SCH.80-FLANGE: WN/RF #150-B16.5	SA106-GR.B SA105-B16.5
N11	1"	1	PI WELL NECK SMLS PIPE SCH.160-FLANGE: WN/RF #300-B16.5	SA106-GR.B SA105-B16.5
N12	2"	1	PSAFETY RELEIF VALVES NECK SMLS PIPE SCH.80-FLANGE: SO/RF #150-B16.5	SA106-GR.B SA105-B16.5
M1A	20"	1	MANHOLE -ROLLED PLATE 10 MM FLANGE SO/RF#150-B16.5	SA516-GR.70 -SA105-B16.5
M1B	20"	1	MANHOLE BLIND FLANGE#150 B16.5 WITH DAVIS ARM AND SUPPORTING HING	SA105
M1C	20"	1	MANHOLE NOZZLE REINFORCEMENT PLATE WIDTH 200 MM X 10 MM THK	SA516-GR.70
M1D	20"	1	MANHOLE DAVIS ARM SOLID BAR 15" SUPPORTING HING PLATE 20MM THK	SA36- SA283-GR.C
S1,2,3	-	1	SHELL PLATES TEIR 1 10 MM X 2500 MM X 6000 MM	SA516-GR.70
H 1/2	-	1	ELLIPTICAL HEADS PLATES 1 & 2 10 MM X1900 X 475 MMX100 MM ST. FLANGE DEFLECTOR PLATE INTERNAL	SA516-GR.70 COLD FORMING
W1	-	1	W1 1350 MM HEIGHT t= 10 mm Defuser Plates QTY 14 x 6 mm thk corrugated	SA516-GR.70
W2,3,4	-	3	WEIR PLATES INTERNALS QTY 3 1400 MM HEIGHT t=10 mm	SA516-GR.70
L	-	2	LIFTING LUGS 20 MM X 150 MM X Ø 50.8 MM HOLE	SA283-GR.C

APPROVED FOR CONSTRUCTION DATE: 04-05-2026

PETROTEC
INDUSTRIAL ENGINEERING COMPANY

3-PHASE SEPARATOR
GENERAL ASSEMBLY - MECHANICAL DETAILS

DWG. NO.	DRAWN BY	DESIGNED BY	DATE
093-2	ENG. I.H	ENG. TAREK HAMMAD	04-May-26

PROPERTY OF PETROTEC. REPRODUCTION OR UNAUTHORIZED USE WITHOUT PRIOR WRITTEN APPROVAL IS PROHIBITED AND SUBJECT TO LEGAL ACTION.