
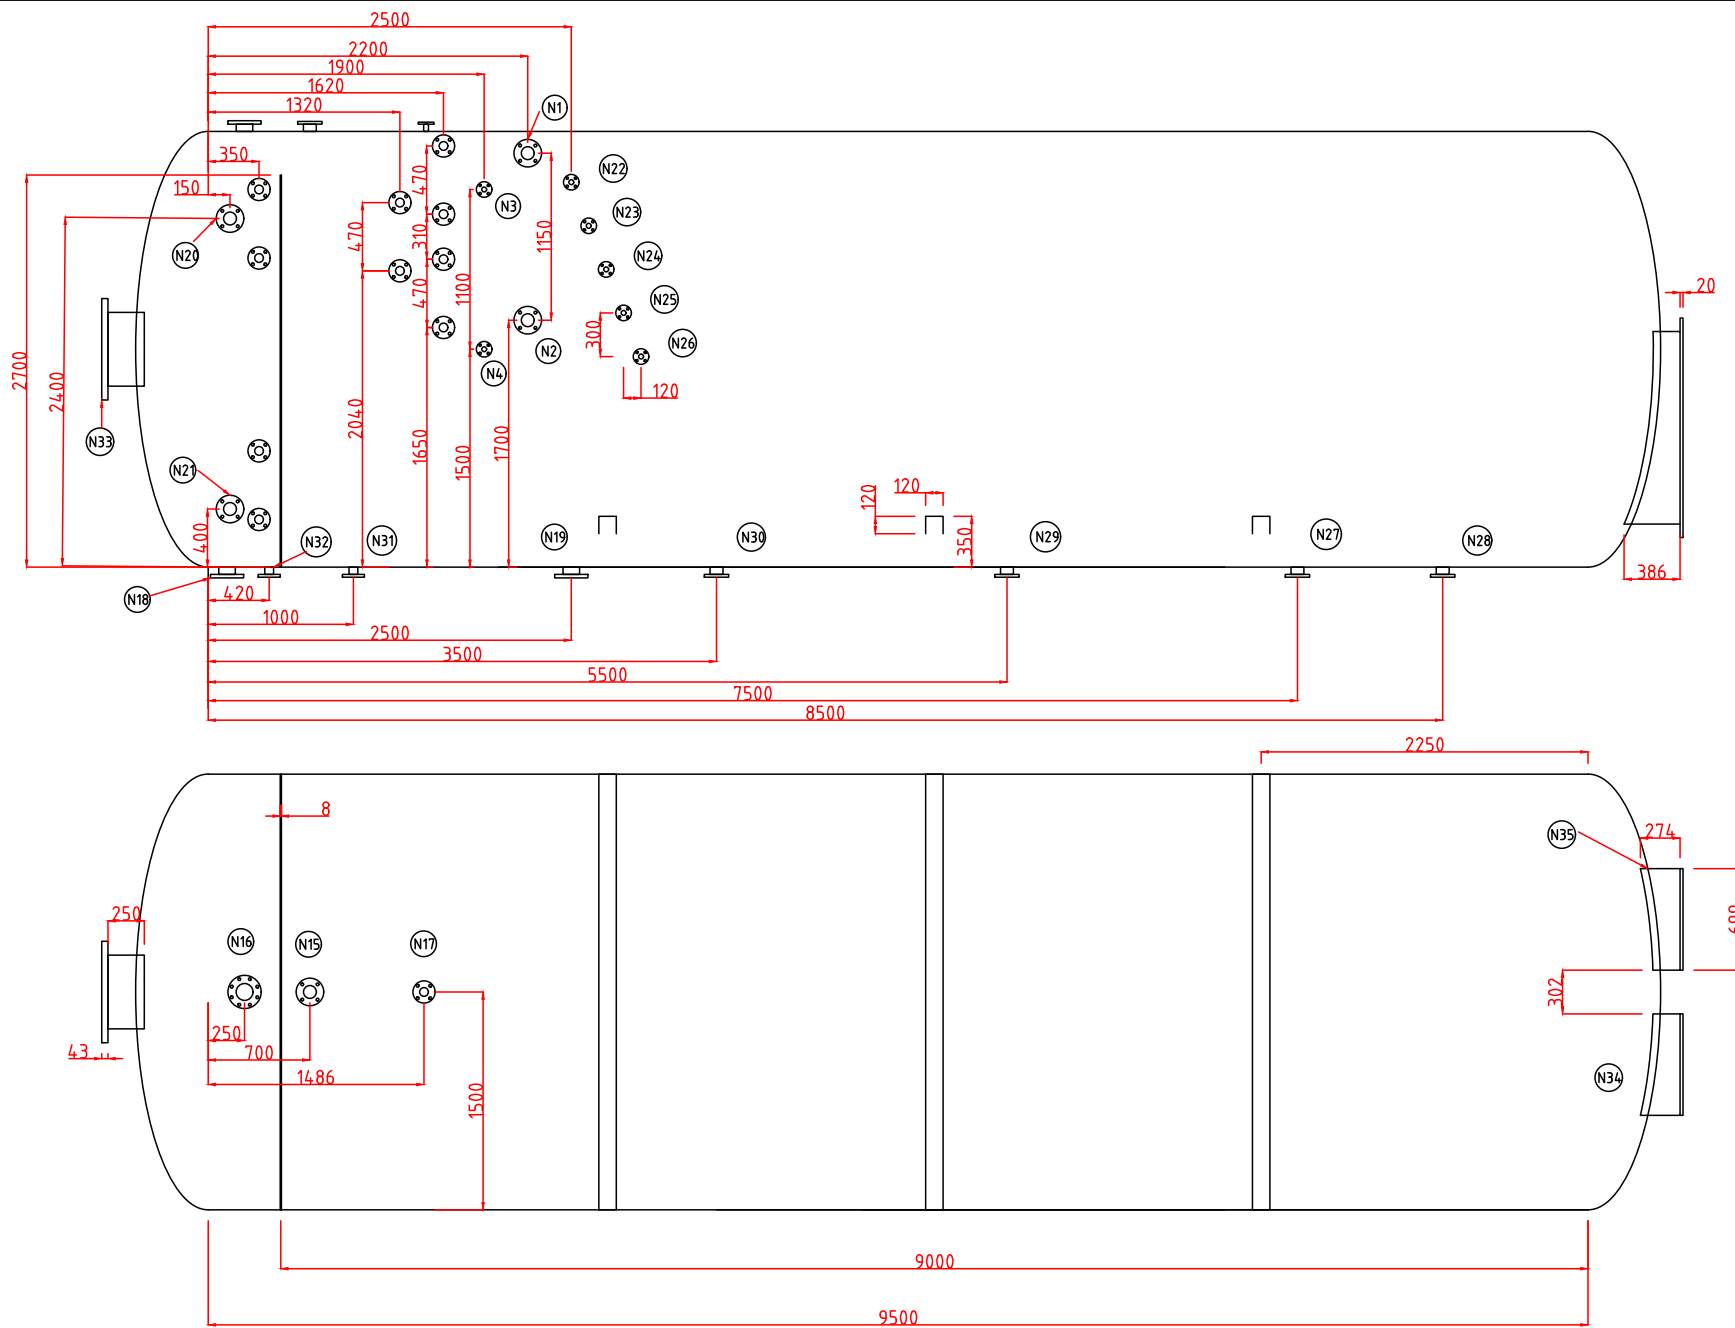
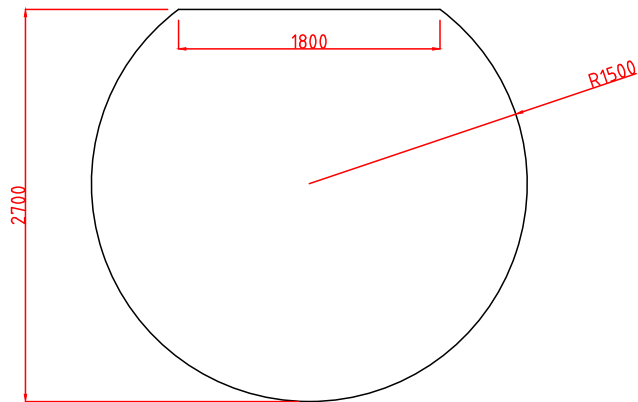
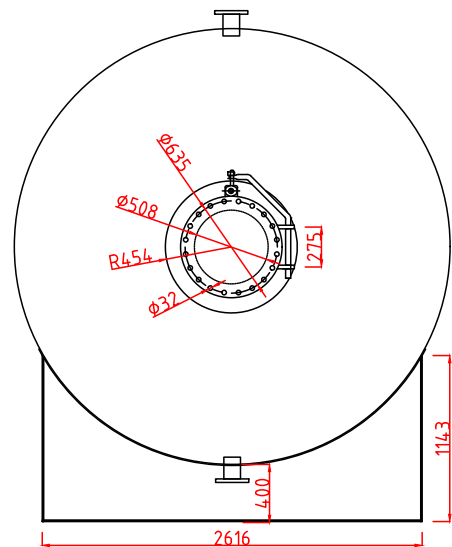


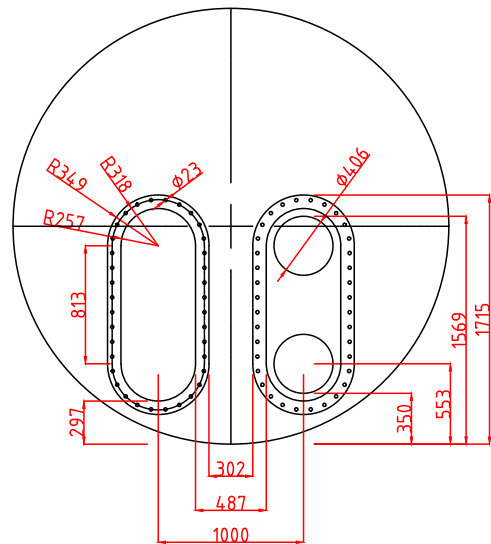

- GENERAL NOTES :
1. CODE OF CONSTRUCTION - ASME SEC.VIII-DIV.I-EDD.2017-STAMPED.
 2. MAWP: For Shell side=75 psig
 3. MDMT=+ 30 F
 4. Hydrotest: Shell side=1.3x75=97.5 psig
for duration of 1/2 hour.
 5. UW-2 FOR LETHAL SERVICE - NON LETHAL .
 6. IMPACT TEST Exempted - UG - 22 (F) , UCS.
 7. Stress Relief exempted as per ASME STD.
 8. Dimension Tolerance as per ASME SEC VIII.
 9. E= 0.60 in Calculation as per ASME STD conditions.

NOZZLE	DIMS	QTY	DESCRIPTION	SPECIFICATION
N1	3"	1	HIGH HIGH LEVEL SWITCH	SA106-GR.B SA105-B16.5
N2	3"	1	LOW LOW LEVEL SWITCH	SA106-GR.B SA105-B16.5
N3 - N4	1"	2	TEMPERATURE TRANSMITTER	SA106-GR.B SA105-B16.5
N5 - N14	2"	10	SIGHT GLASS	SA106-GR.B SA105-B16.5
N15	3"	1	PRESSURE SAFETY VALVE	SA106-GR.B SA105-B16.5
N16	4"	1	GAS OUTLET	SA106-GR.B SA105-B16.5
N17	2"	1	PRESSURE GAUGE	SA106-GR.B SA105-B16.5
N18	4"	1	OIL OUTLET	SA106-GR.B SA105-B16.5
N19	4"	1	CRUDE OIL INPUT	SA106-GR.B SA105-B16.5
N20 - N21	3"	2	OIL LEVEL SWITCHES	SA106-GR.B SA105-B16.5
N22 - N26	1"	5	SAMPLING NOZZLE	SA106-GR.B SA105-B16.5
N27	3"	1	FRESH WATER INLET	SA106-GR.B SA105-B16.5
N28 - N31	3"	4	WATER DRAIN	SA106-GR.B SA105-B16.5
N32	2"	1	WATER DRAIN	SA106-GR.B SA105-B16.5
N33	20"	1	MANHOLE NECK ROLLED PLATE 10MM	SA516-GR.70 SA105-B16.5
N34 - N35	20"	2	FIRETUBE FLANGE OPENING	SA516-GR.70 SA105-B16.5

APPROVED FOR CONSTRUCTION DATE: 04-05-2026

PETROTEC

INDUSTRIAL ENGINEERING COMPANY

HEATER TREATER
GENERAL ASEMBLY - MECHANICAL DETAILS

DWG. NO.	DRAWN BY	DESIGNED BY	DATE
PT-092-2	ENG. I.H	ENG. TAREK HAMMAD	04-May-26

